


Passmass	Abmass

Schnitt A-B
SECTION

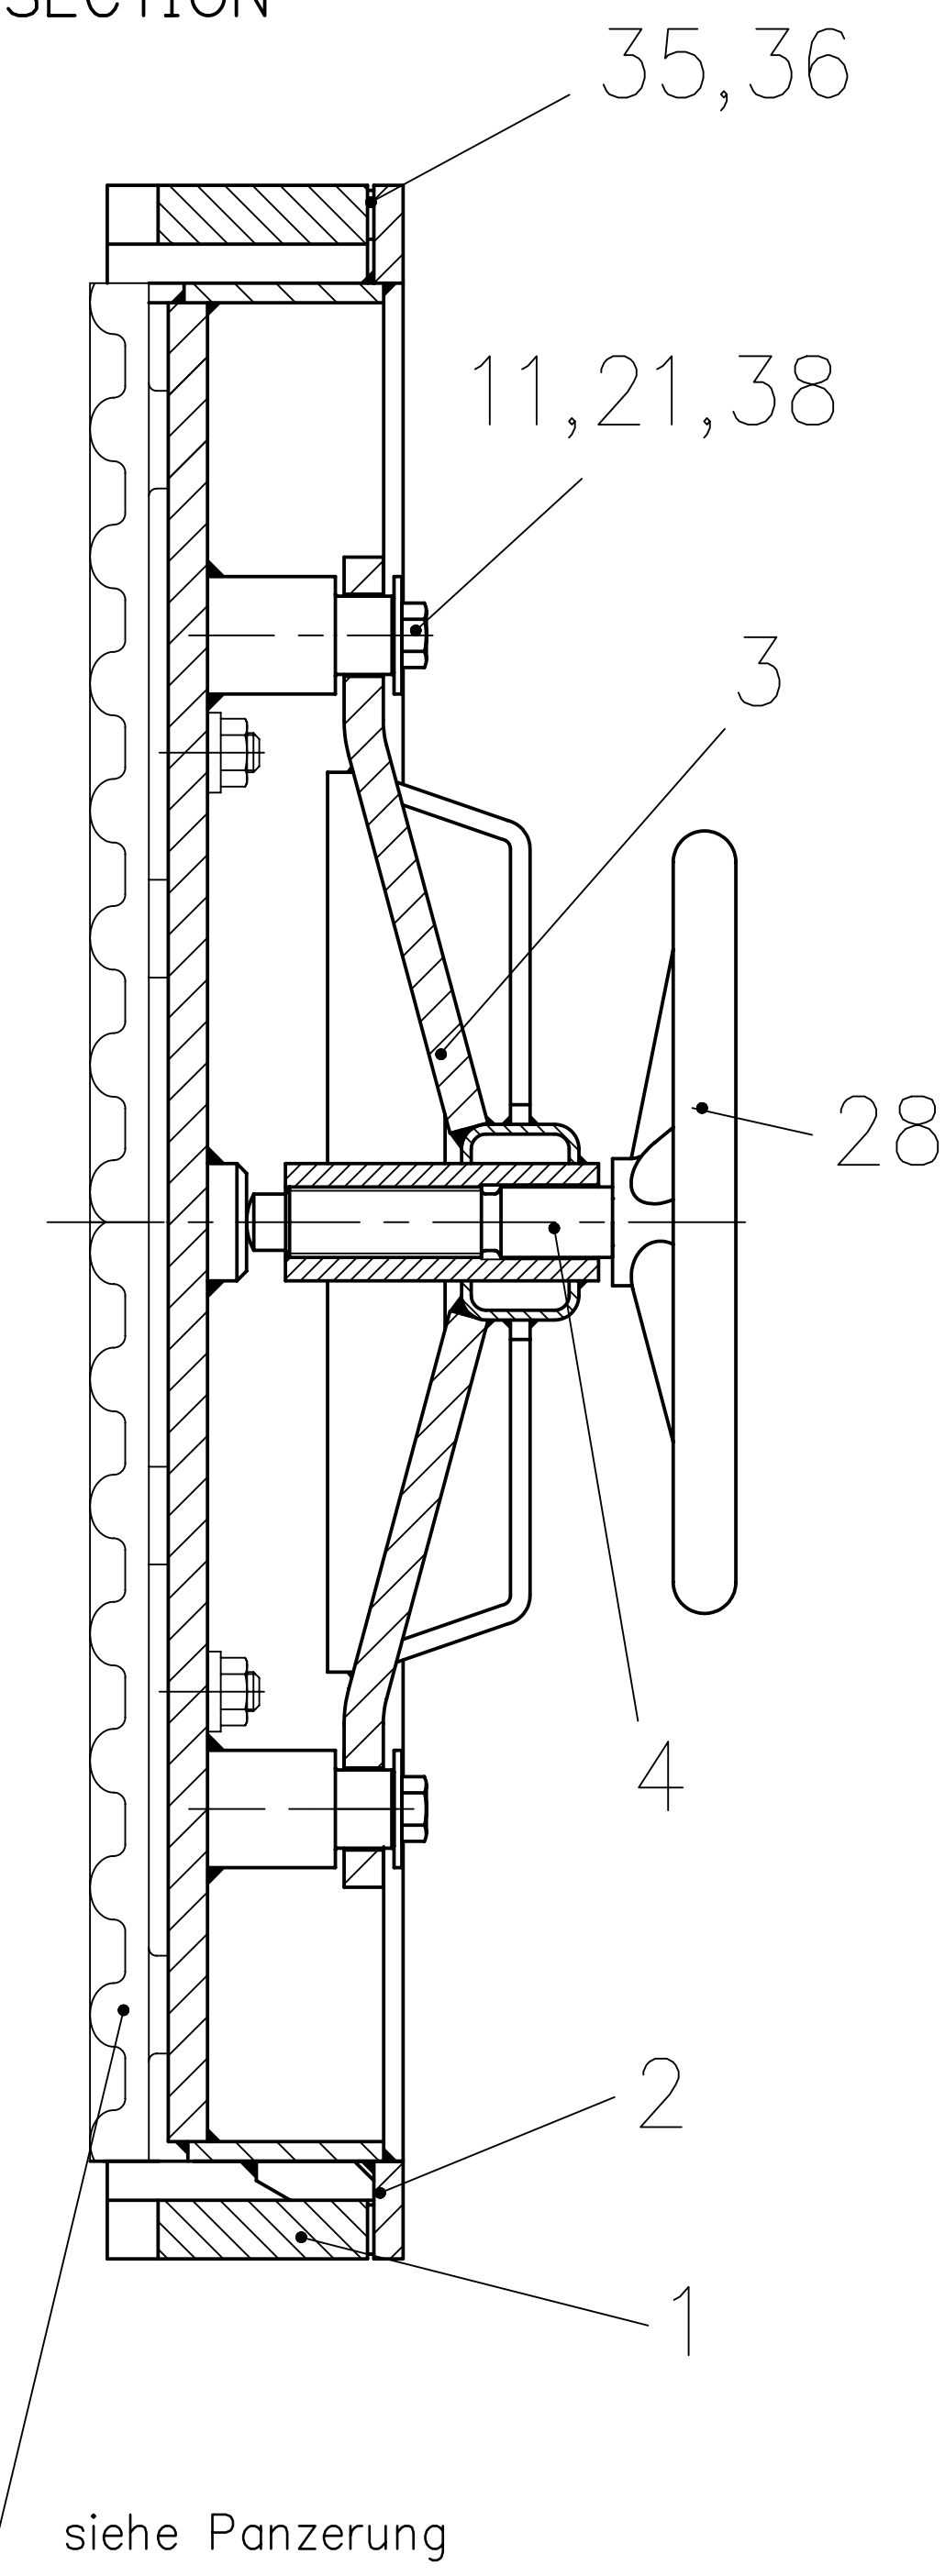


SEE LINING

siehe Panzerung

SEE LINING

Schnitt C-D
SECTION

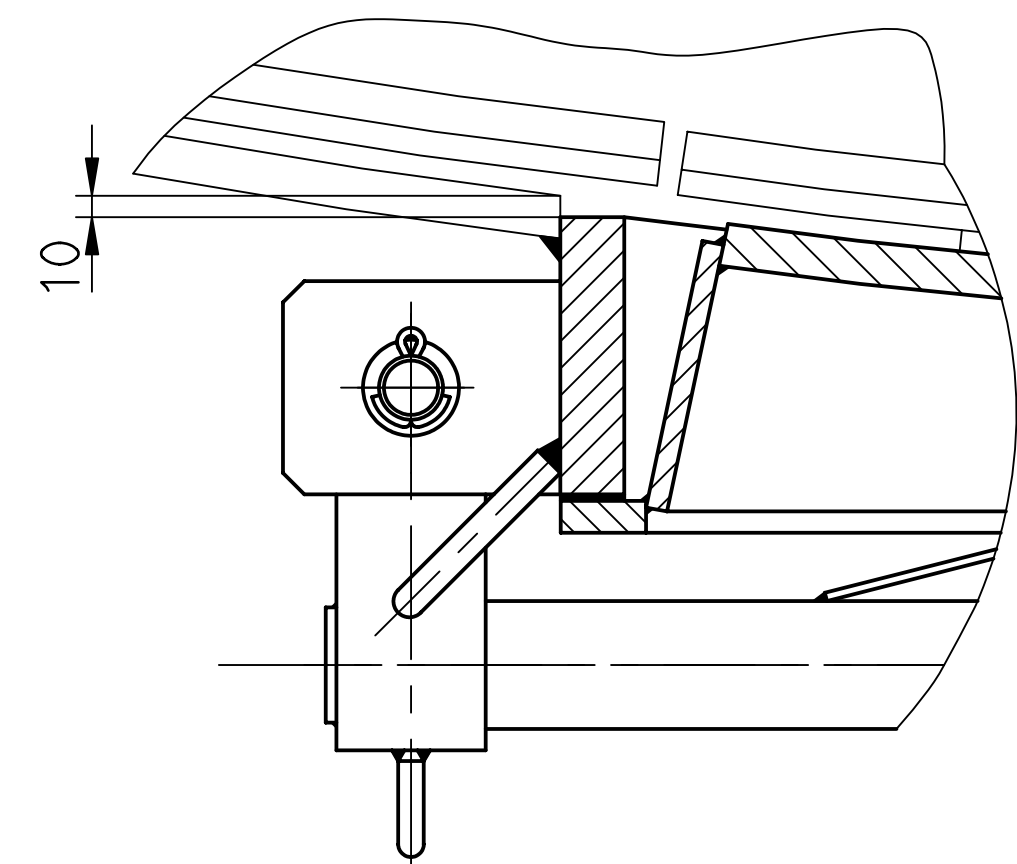

CAD erstellte Zeichnung

Ges.-Gew.		352.-kg		Betreff:				Suchbez.							
Gez.	25.10.93 Sh			Ersatz für				LOESCHE							
Gepr.	27.10.93 Pe			Ersetzt durch											
Gez.				File-Nr. :Z0004793											
Gepr.															
Oberflächenzeichen Mittenrauhwert R_a in μm Masse ohne Toleranzangaben nach DIN 7168 Gütegrad mittel				✓ Anlieferzustand	✓ $Ra \leq 50$	W $Ra \leq 12,5$	X $Ra \leq 1,6$	Y $Ra \leq 0,4$	Z $Ra \leq 0,1$	Ident: 020170-00-2		CAD		EDV	
Masstab 1:5				MUEHLENTUER KPL 1000x800/R1600-<R3600					003905-00-2						
				MILL DOOR CPL.					Urheberschutz nach DIN34 vorbehalten		Total	Bl.	Bl.Nr.		



CAD

EDV