


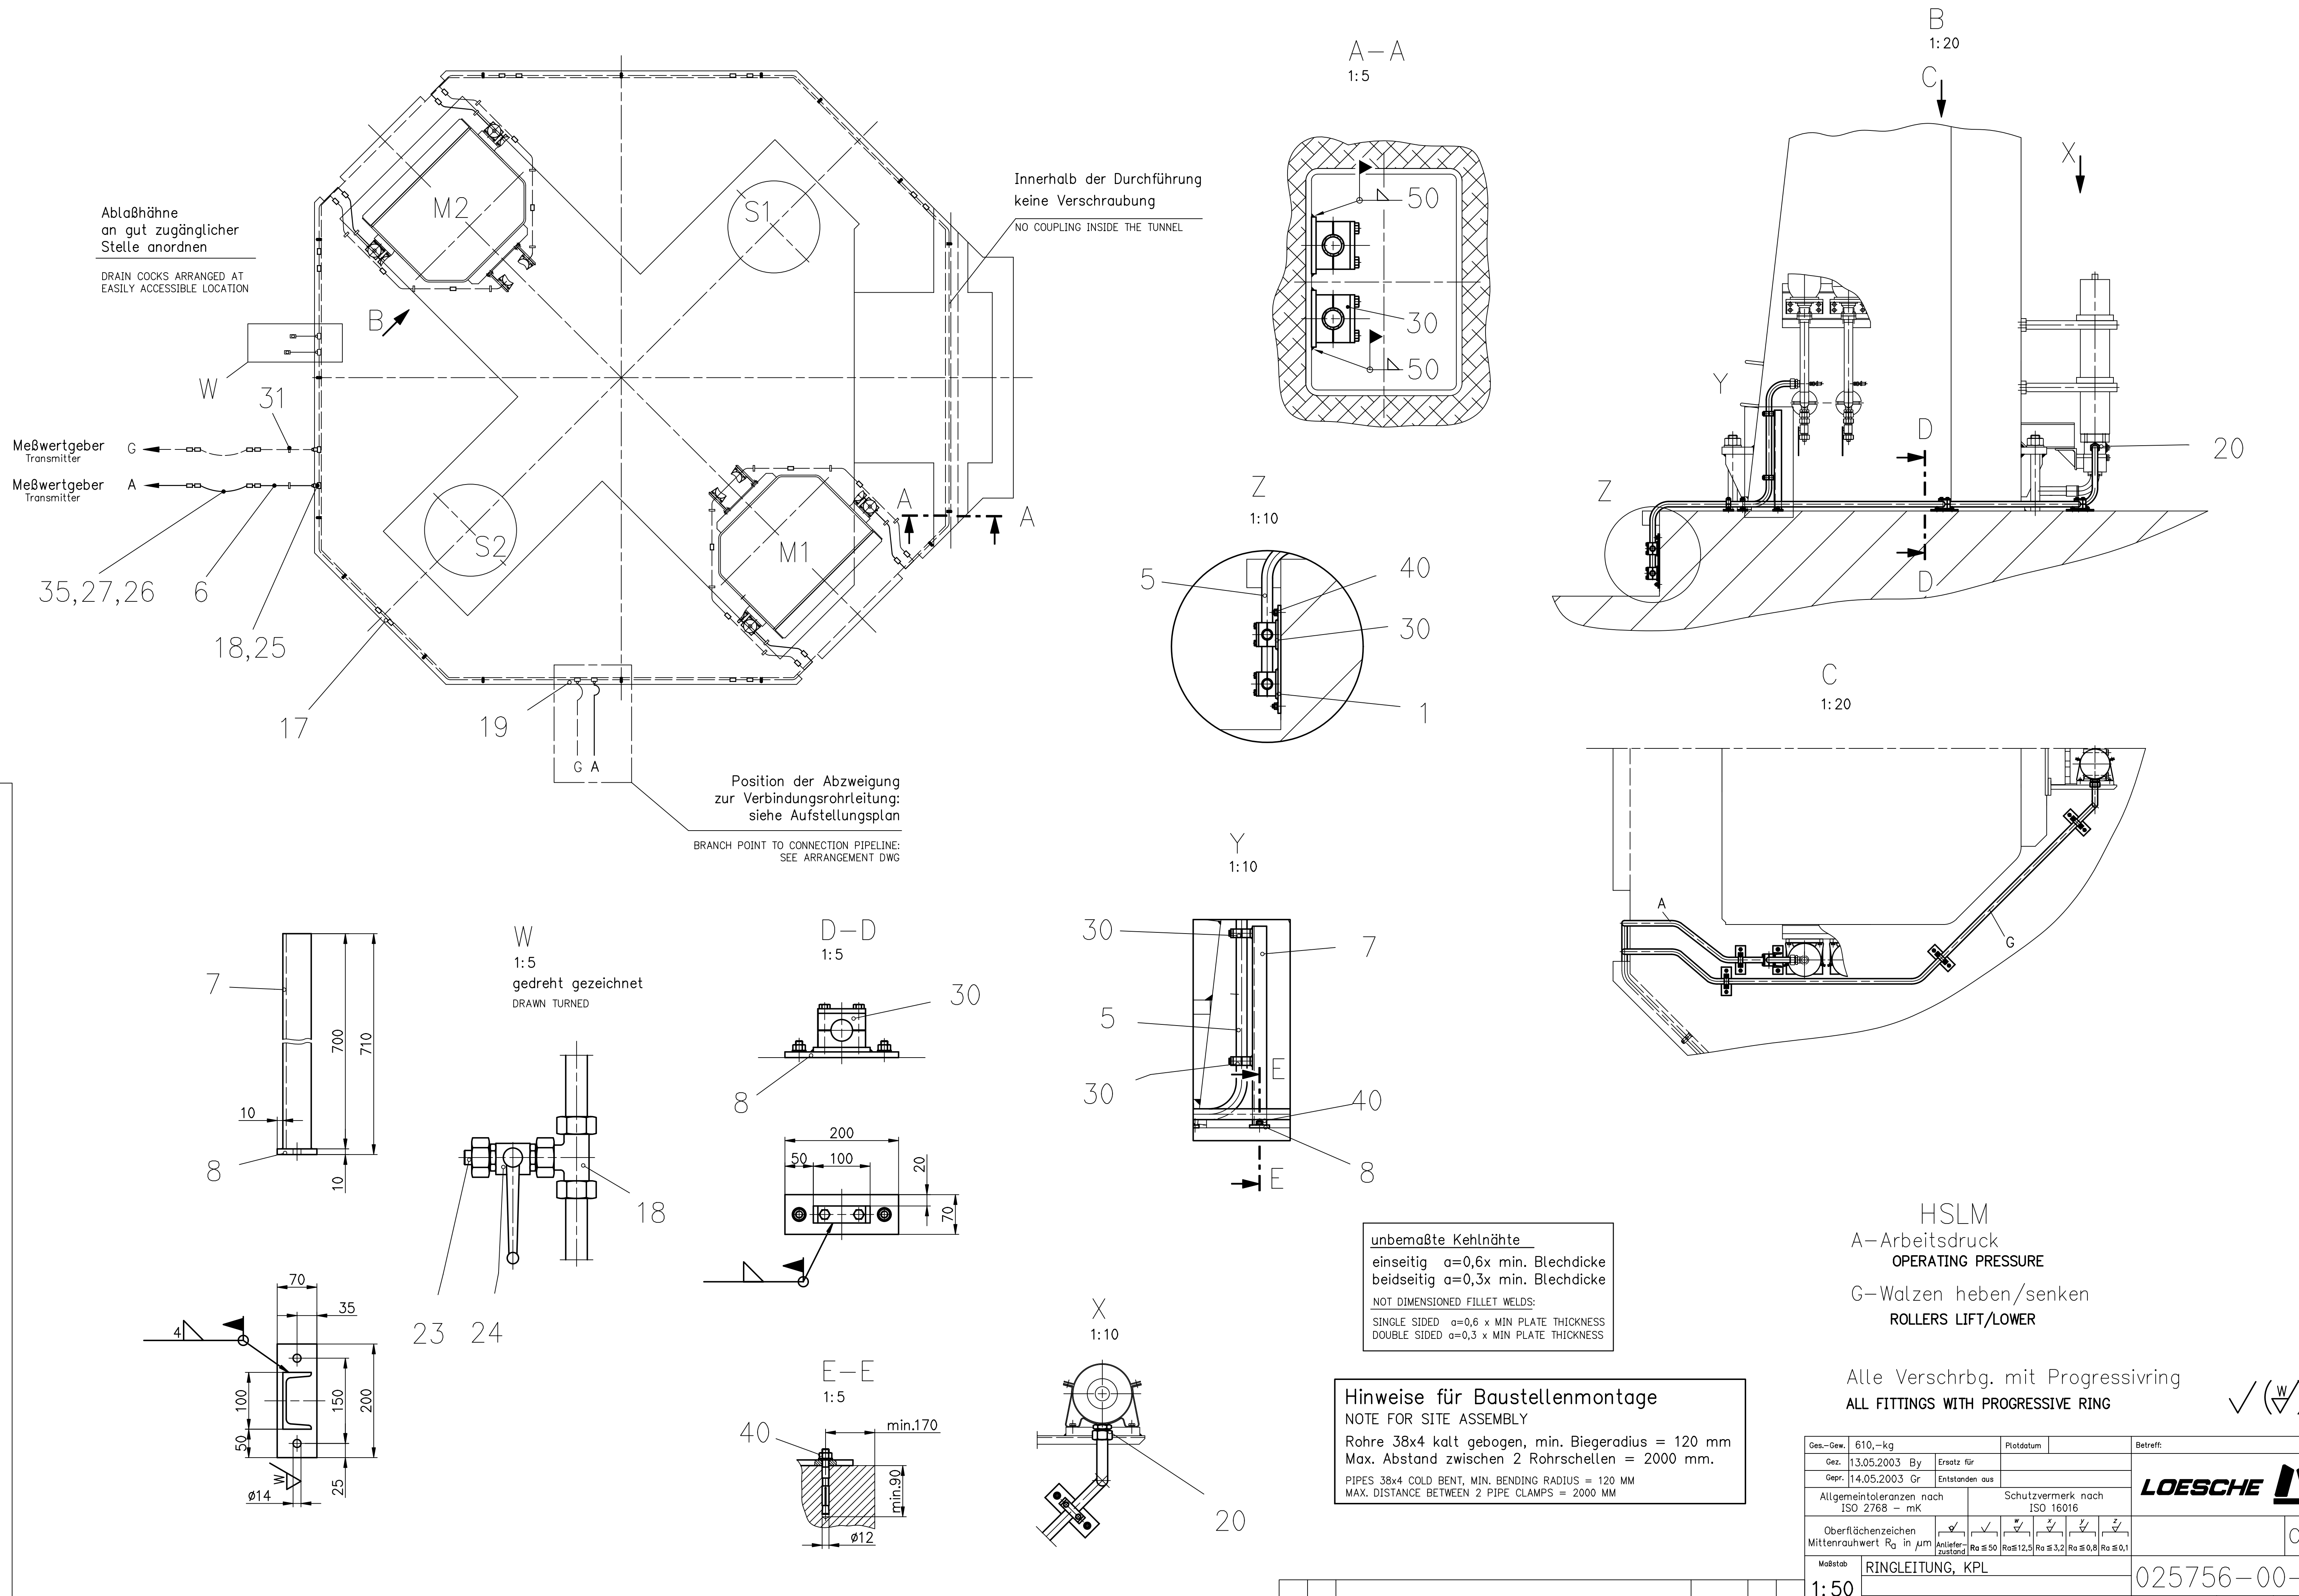

A—A
1:5

B
1:20

C

X

20

C
1:20

Z
1:10

Y
1:10

D—D
1:5

W
1:5
gedreht gezeichnet
DRAWN TURNED

30

5

30

8

40

8


20

unbemaßte Kehlnähte
einseitig $a=0,6 \times \text{min. Blechdicke}$
beidseitig $a=0,3 \times \text{min. Blechdicke}$
NOT DIMENSIONED FILLET WELDS:
SINGLE SIDED $a=0,6 \times \text{MIN PLATE THICKNESS}$
DOUBLE SIDED $a=0,3 \times \text{MIN PLATE THICKNESS}$

Hinweise für Baustellenmontage
NOTE FOR SITE ASSEMBLY
Rohre 38x4 kalt gebogen, min. Biegeradius = 120 mm
Max. Abstand zwischen 2 Rohrschellen = 2000 mm.
PIPES 38x4 COLD BENT, MIN. BENDING RADIUS = 120 MM
MAX. DISTANCE BETWEEN 2 PIPE CLAMPS = 2000 MM

HSLM
A—Arbeitsdruck
OPERATING PRESSURE
G—Walzen heben/senken
ROLLERS LIFT/LOWER

Alle Verschrbg. mit Progressivring
ALL FITTINGS WITH PROGRESSIVE RING

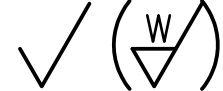

Ges.-Gew.	610,—kg	Plattdatum		Betreff:	
Gez.	13.05.2003	By	Ersatz für		
Gepr.	14.05.2003	Gr	Entstanden aus		
Allgemeintoleranzen nach ISO 2768 - mK				Schutzvermerk nach ISO 16016	
Oberflächenzeichen				CAD	
Mittenrauhwert R_a in μm				025756-00-1	
Maßstab				1:50	
RINGLEITUNG, KPL				RING PIPELINE, CPL	
				Total	