





THE INFORMATION CONTAINED HEREIN IS THE PROPERTY OF LOESCHE. IT IS TO BE USED FOR THE EXCLUSIVE PURPOSE OF THE PROJECT FOR WHICH IT WAS PREPARED. IT IS NOT TO BE REPRODUCED, COPIED, OR TRANSMITTED IN ANY FORM OR BY ANY MEANS, ELECTRONIC OR MECHANICAL, INCLUDING PHOTOCOPYING, RECORDING, OR BY ANY INFORMATION STORAGE AND RETRIEVAL SYSTEM. WITHOUT THE WRITTEN PERMISSION OF LOESCHE, NO PART OF THIS DOCUMENT IS TO BE REPRODUCED OR TRANSMITTED IN ANY FORM OR BY ANY MEANS, ELECTRONIC OR MECHANICAL, INCLUDING PHOTOCOPYING, RECORDING, OR BY ANY INFORMATION STORAGE AND RETRIEVAL SYSTEM.


Alle Angaben sind verbindlich. Diese Zeichnung, Verweisung und Maßangaben sind verbindlich. 

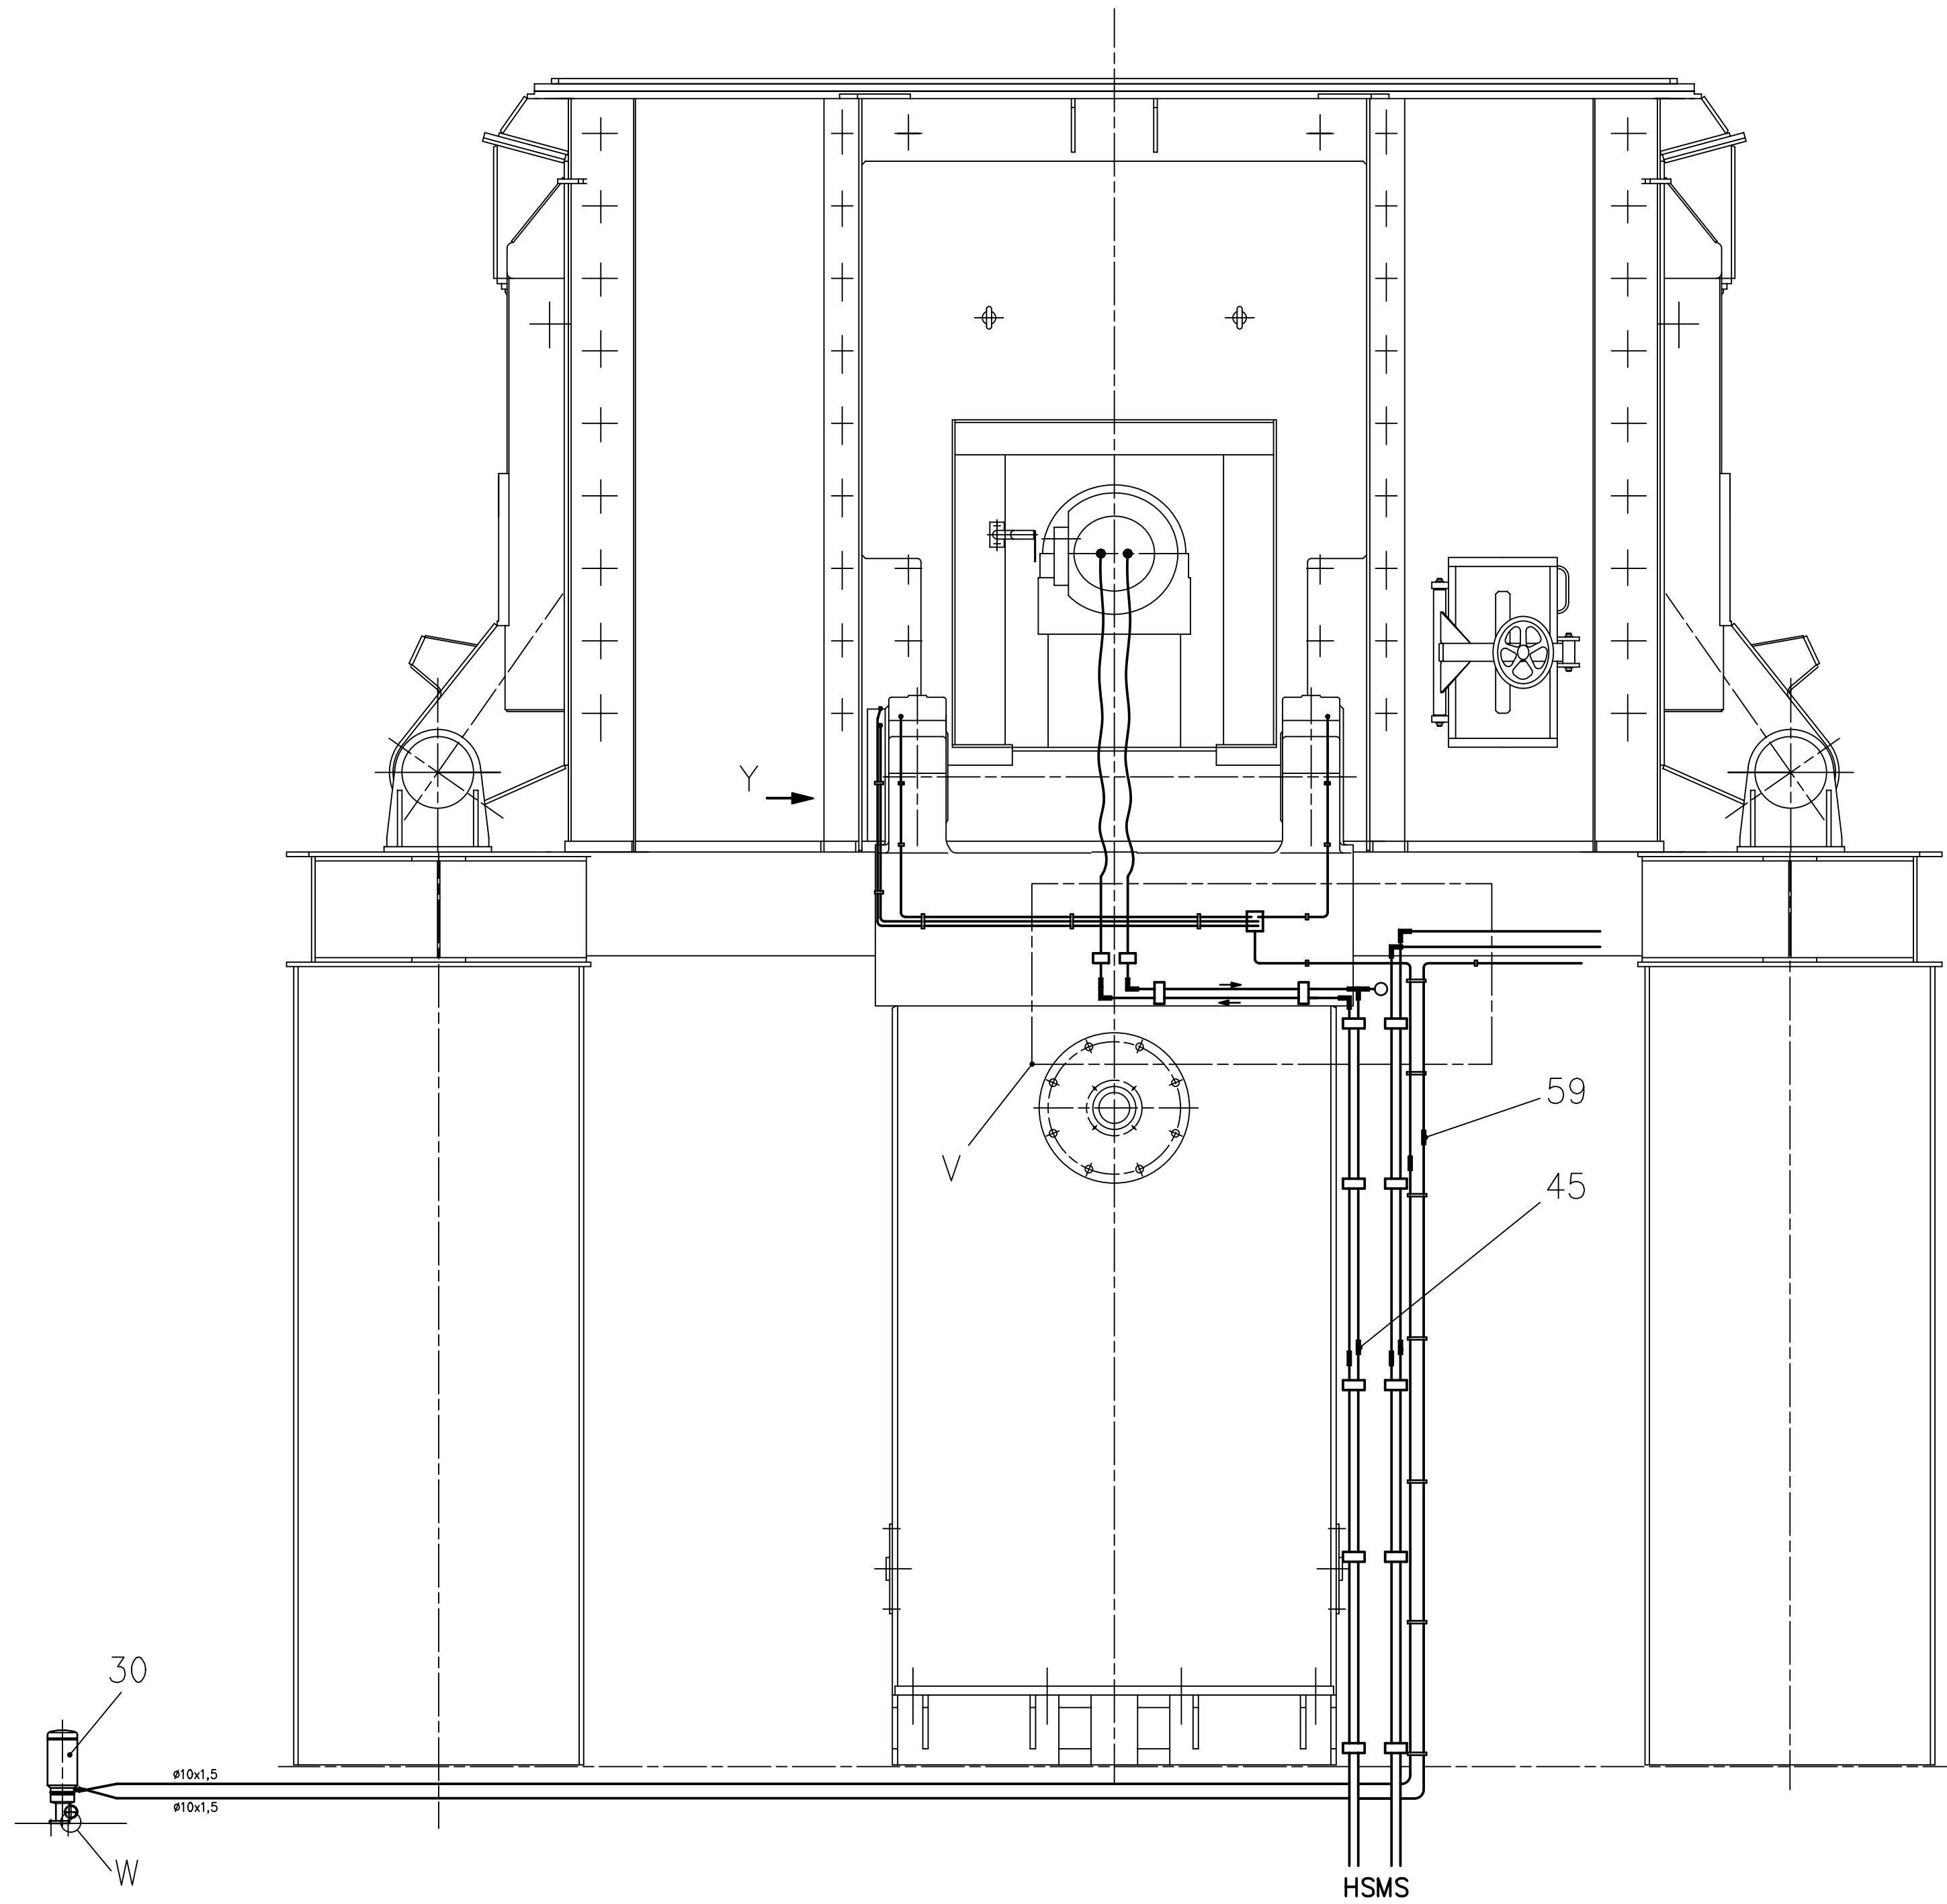

Bei der Baustellenmontage der Leitungen auf den Ausschwenkbock achten!
AT SITE ASSEMBLY OF THE PIPELINE, PAY ATTENTION FOR THE SWINGING-OUT BLOCK!

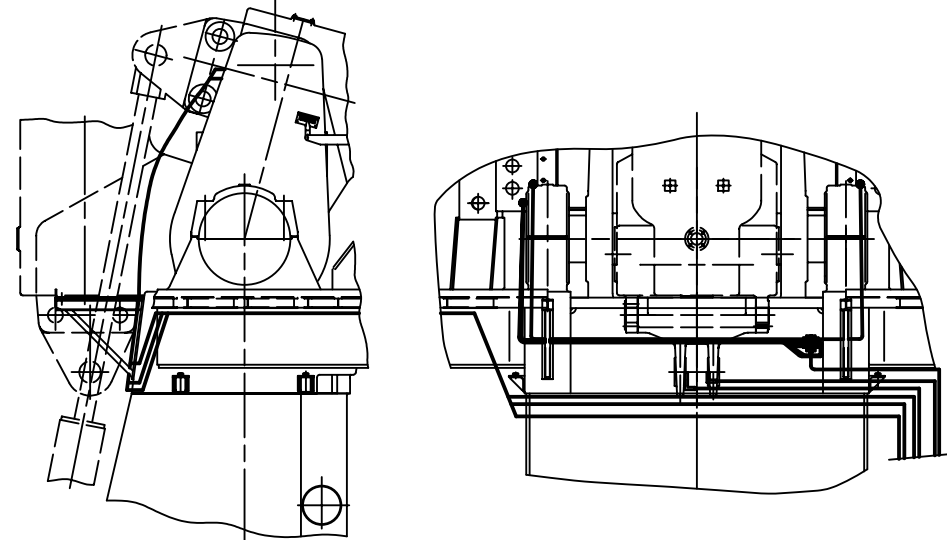


Schutzbleche gegen Strahlungswärme
im Bereich der Gaskanäle
COVER PLATE AGAINST RADIANT HEAT
IN THE AREA OF GAS DUCTS

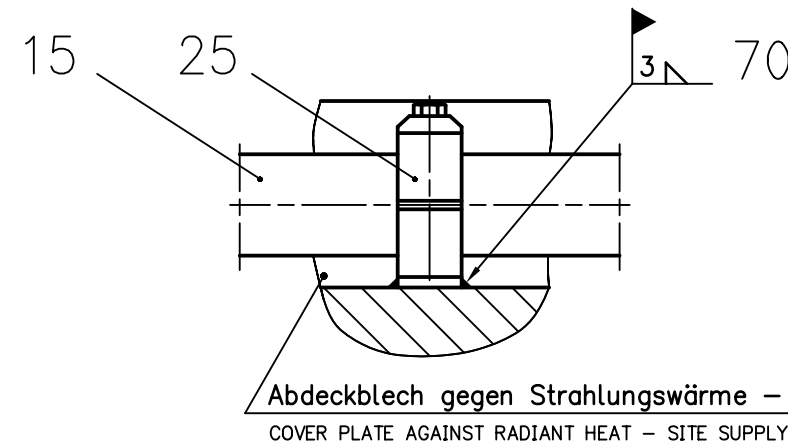


Abdeckblech gegen Strahlungswärme – bauseitig
COVER PLATE AGAINST RADIANT HEAT – SITE SUPPLY


Einzelheit W
DETAIL
M 1:2

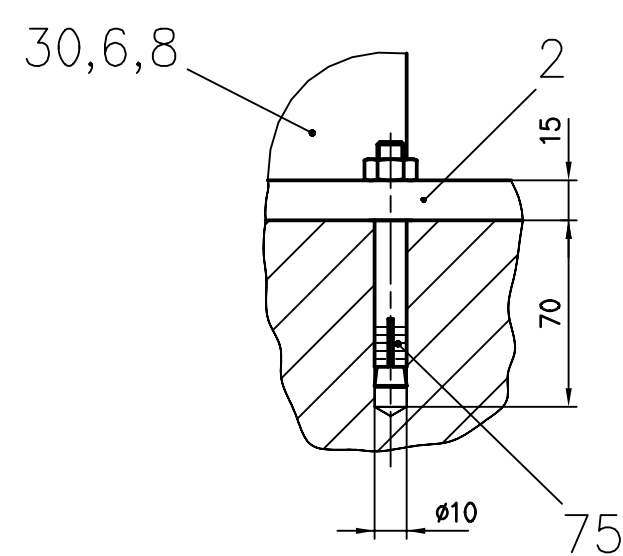


Ansicht Y
VIEW
M 1:10

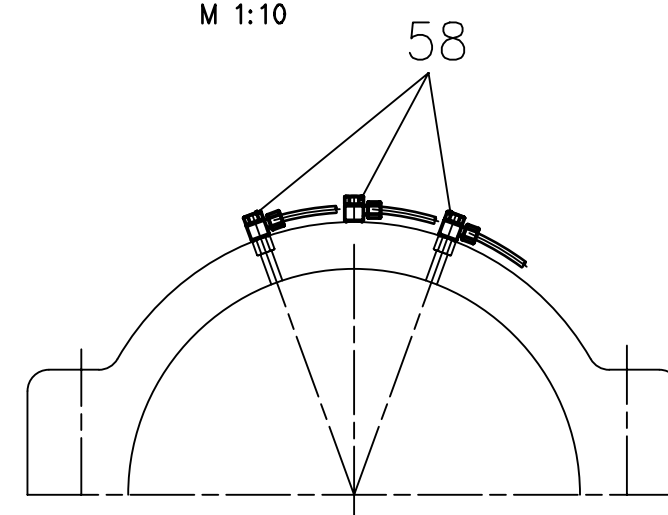

Einzelheit V
DETAIL
M 1:5

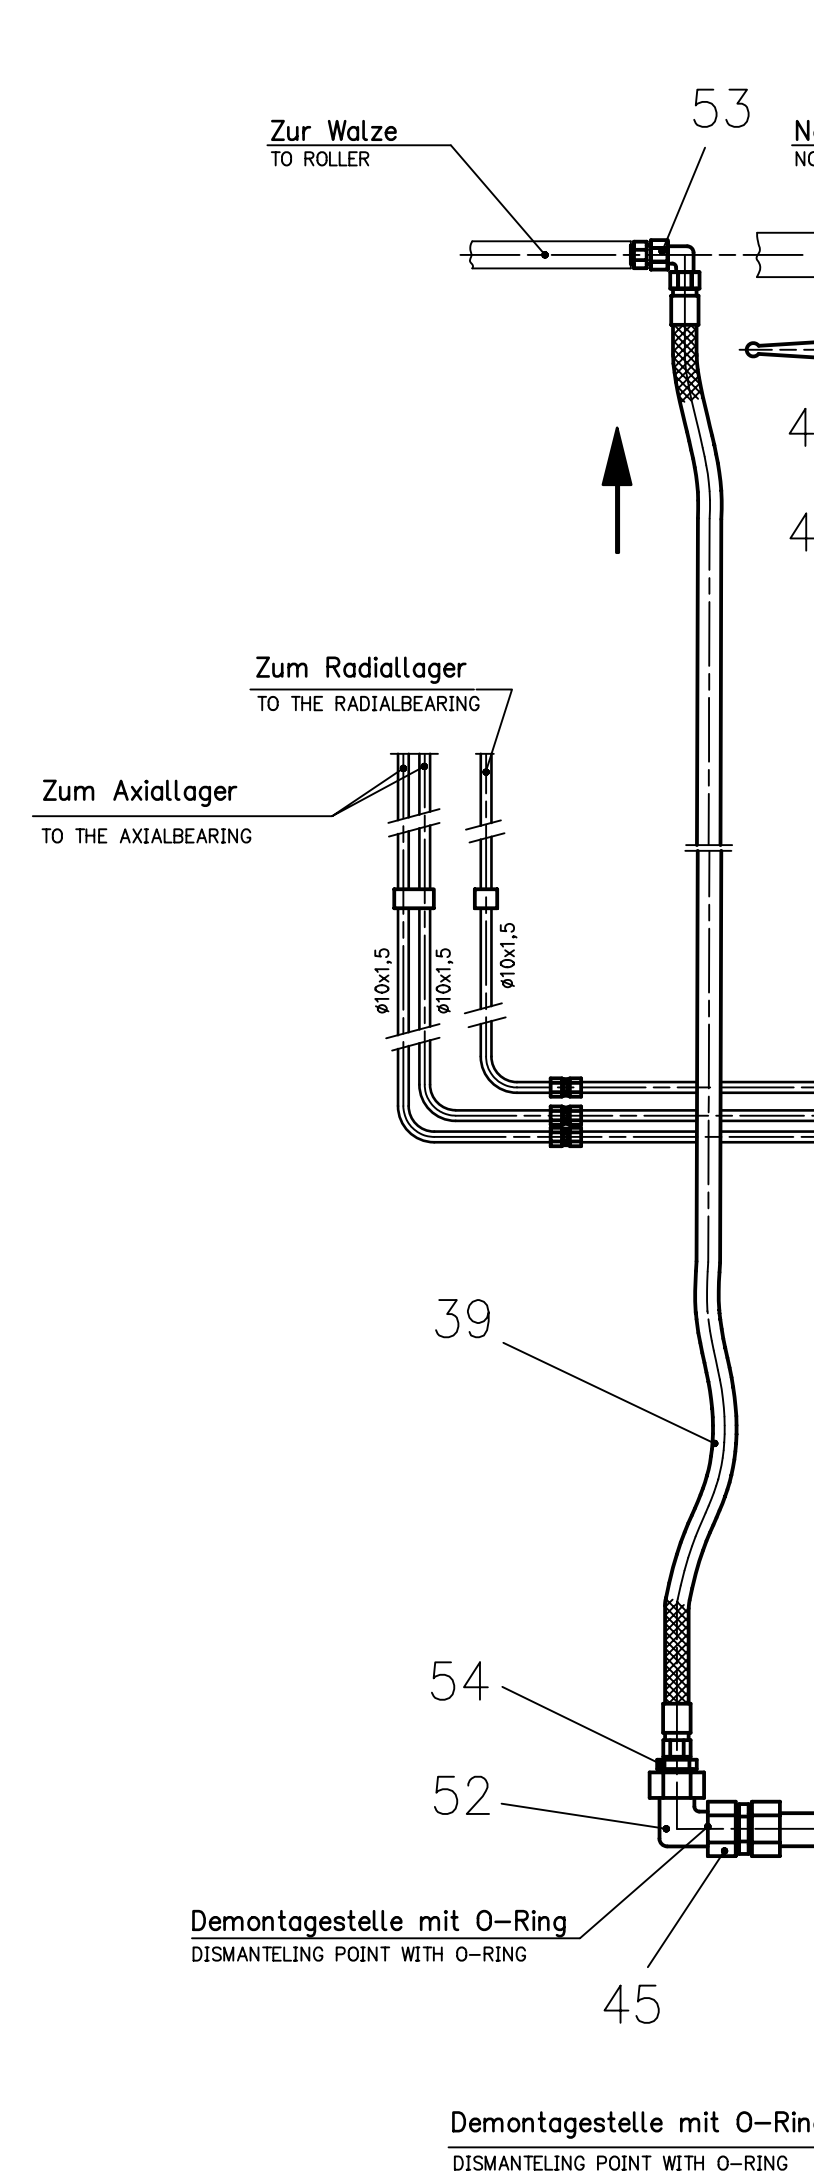


Einzelheit Z
DETAIL
M 1:2

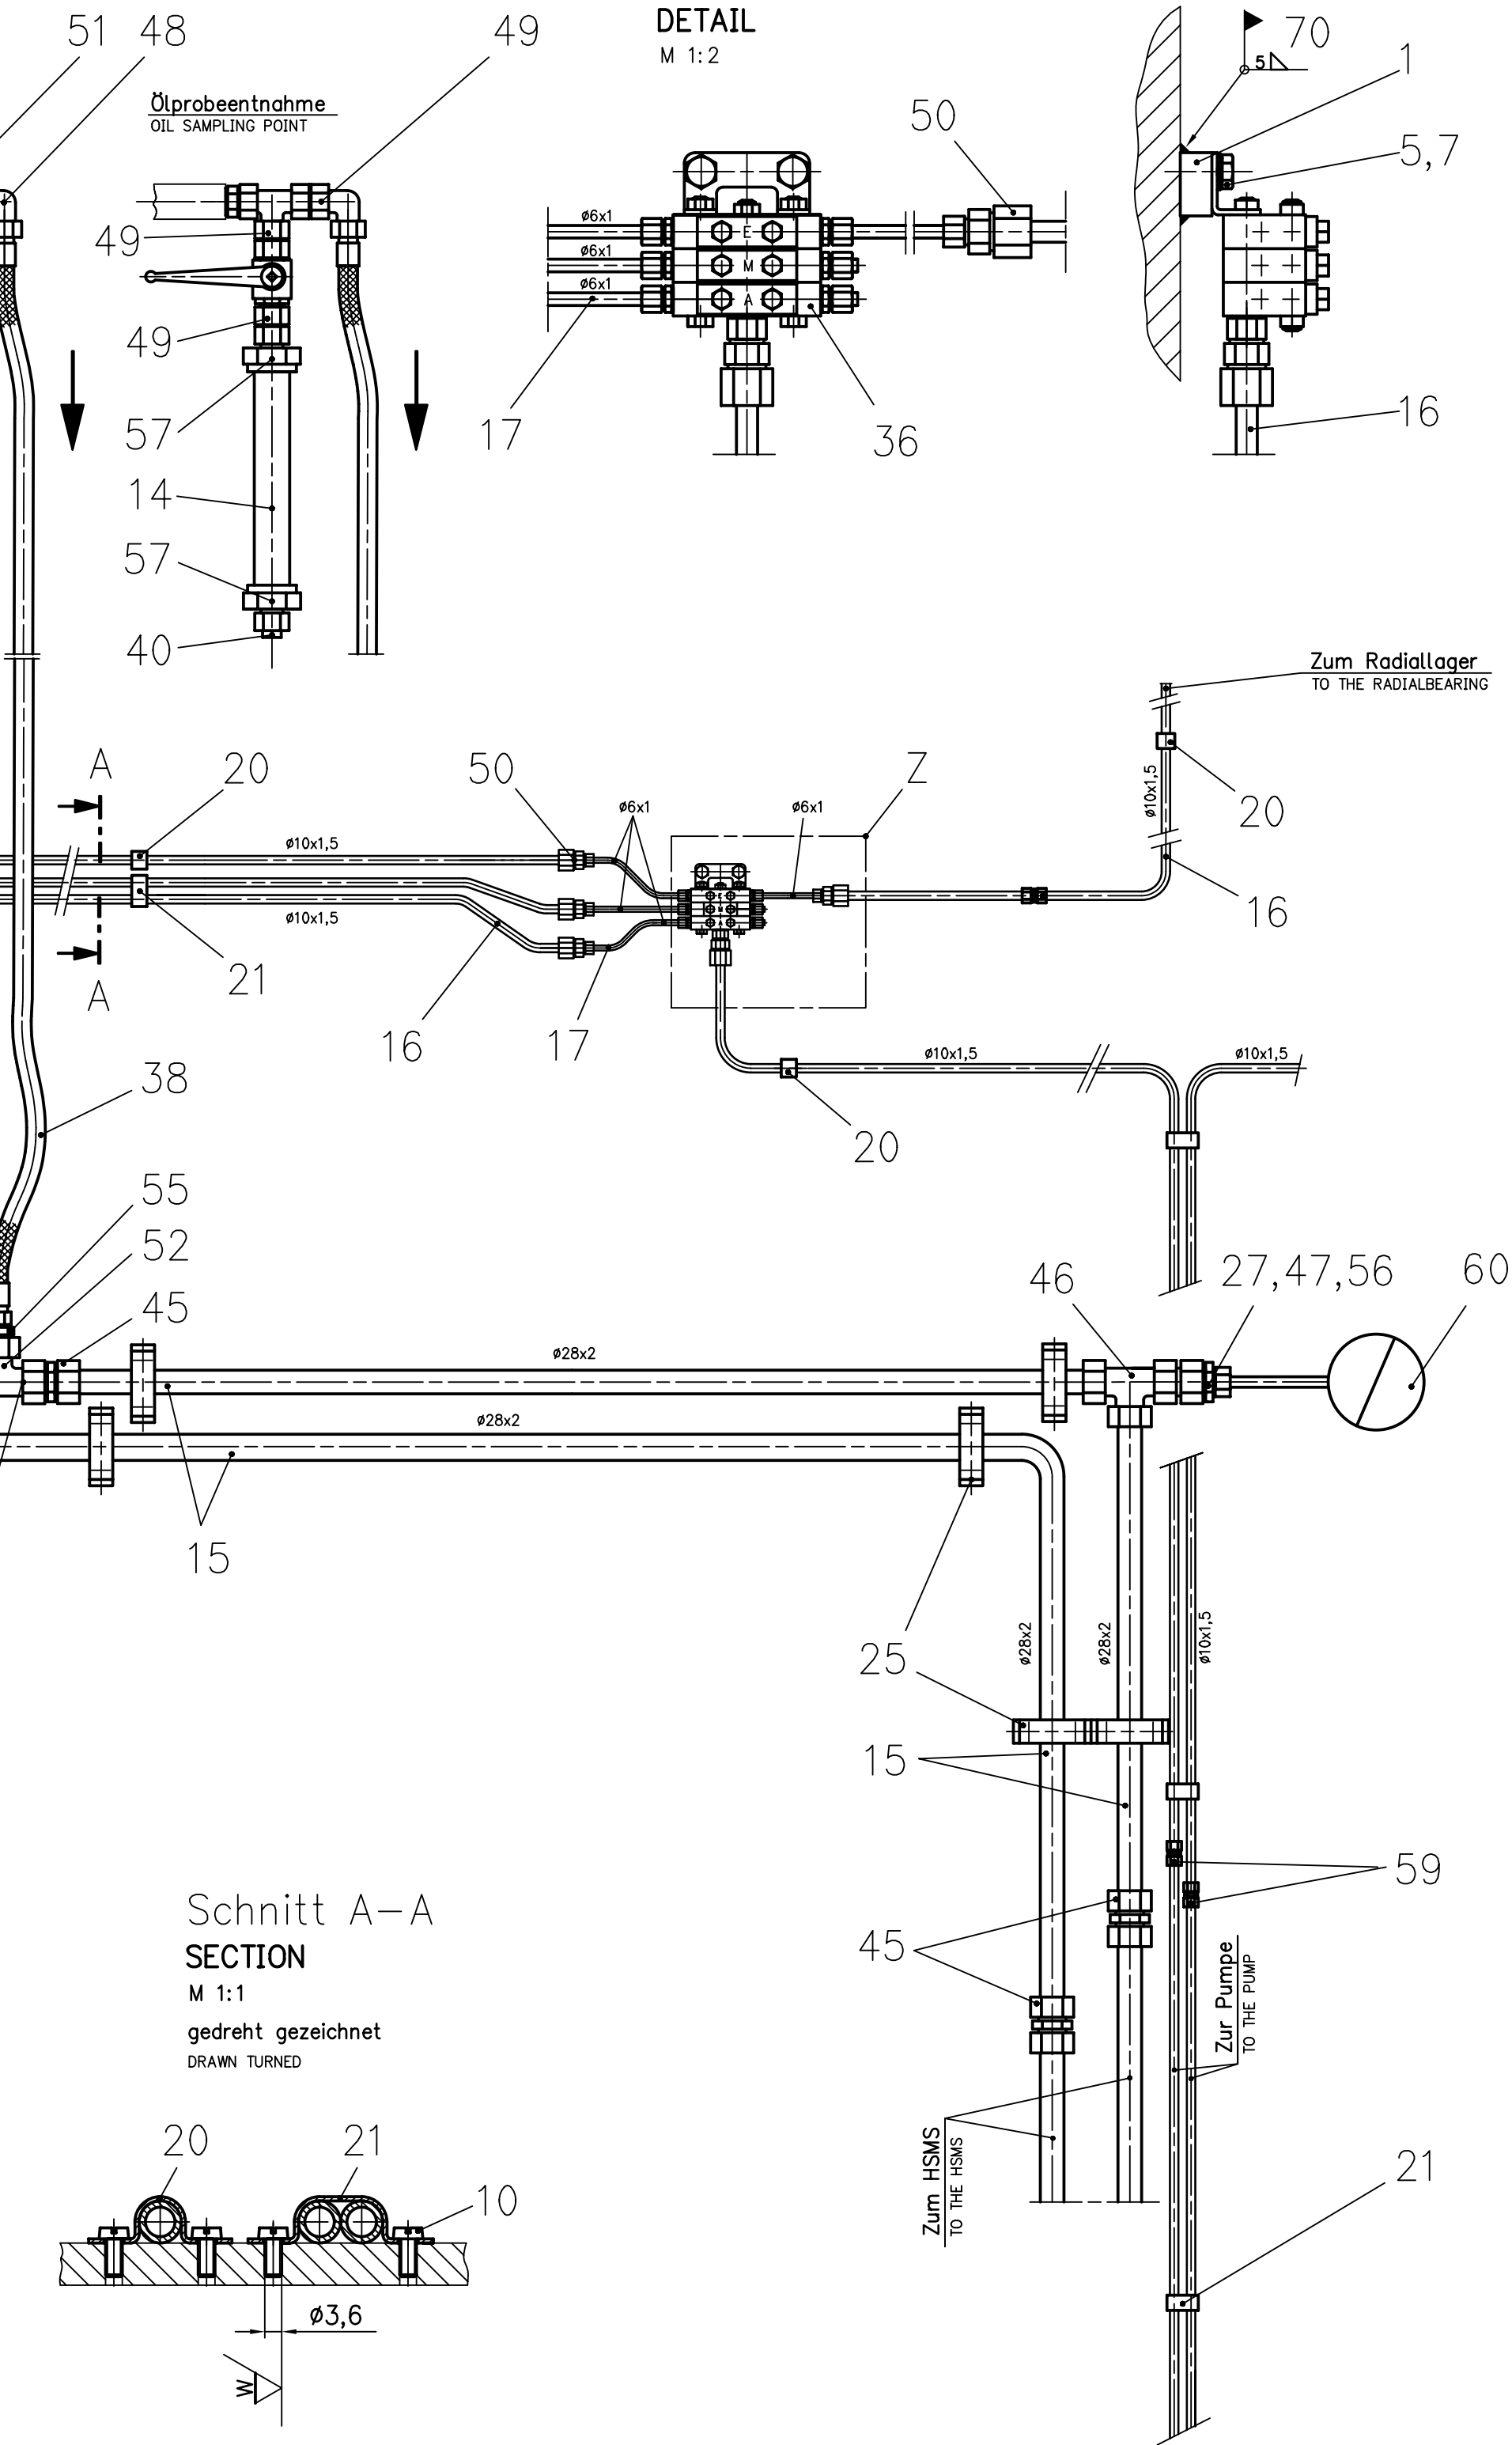

Schnitt A-A
SECTION
M 1:1

gedreht gezeichnet
DRAWN TURNED

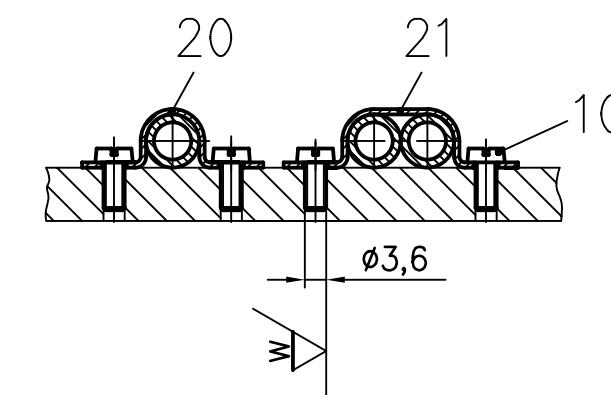

Unberaßte Kehlnähte
Einseitig $\alpha=0,6 \times \text{min. Blechdicke}$
Beidseitig $\alpha=0,3 \times \text{min. Blechdicke}$
NOT DIMENSIONED FILLET WELDS:
SINGLE SIDED $\alpha=0,6 \times \text{min. PLATE THICKNESS}$
DOUBLE SIDED $\alpha=0,3 \times \text{min. PLATE THICKNESS}$

Hinweise für Baustellenmontage
NOTE FOR SITE ASSEMBLY

Rohre 28x2 kalt gebogen, min. Biegeradius = 90 mm
Max. Abstand zwischen 2 Rohrschellen = 1500 mm.
PIPES 28x2 COLD BENT, MIN. BENDING RADIUS = 90 MM
MAX. DISTANCE BETWEEN 2 PIPE CLAMPS = 1500 MM
Rohre 10x1,5 kalt gebogen, min. Biegeradius = 35 mm
Max. Abstand zwischen 2 Rohrschellen = 1200 mm.
PIPES 10x1,5 COLD BENT, MIN. BENDING RADIUS = 35 MM
MAX. DISTANCE BETWEEN 2 PIPE CLAMPS = 1200 MM
Rohre 6x1 kalt gebogen, min. Biegeradius = 25 mm
PIPES 6x1 COLD BENT, MIN. BENDING RADIUS = 25 MM

ersetzt durch Zeichnung mit nächst
höherem Änderungsindex!!!
DRAWING REPLACED BY NEXT HIGHER REVISION!!!

Montage der Fettschmierleitungen nach
Schema (Siehe Stückliste)
ASSEMBLY OF THE GREASE LUBRICATION LINE
ACCORDING TO SCHEME (SEE PART LIST)



Allgemeine Toleranzen nach GENERAL TOLERANCES ACC TO		ISO 2768 – mK	
Brennschneitten FLAME CUTS		nach ACC TO	
Schweißkonstruktion WEILED CONSTRUCTION		nach ACC TO	
Schweißnahtvorrichtung EDGE PREPARATION FOR WELDING		nach ACC TO	
Schweißnahtverbindung FUSION WELDED		nach ACC TO	
Oberflächenzeichen SURFACE FINISH MARK		nach ACC TO	
Werkstückkanten nach COMPONENT EDGES ACC TO		nach ACC TO	
Maßstab SCALE		1:25	
LM-SCHMIERLEITUNG; KPL. 2 WALZEN (LM ... C/S) LM-LUBRICATION LINE; CPL.		LM-SCHMIERLEITUNG; KPL. 2 WALZEN (LM ... C/S) LM-LUBRICATION LINE; CPL.	
Datum / DATE		12.07.2004	
Gezeichnet / DRAWN		By	
Geprüft / CHECKED		14.07.2004	
Geprüft / CHECKED		dk	
Total / TOTAL		025810-00-0	
Bl. / SRT		BL. / SRT	
SRT / SHT		SHT / SHT	
SHT / SHT		SHT / SHT	