




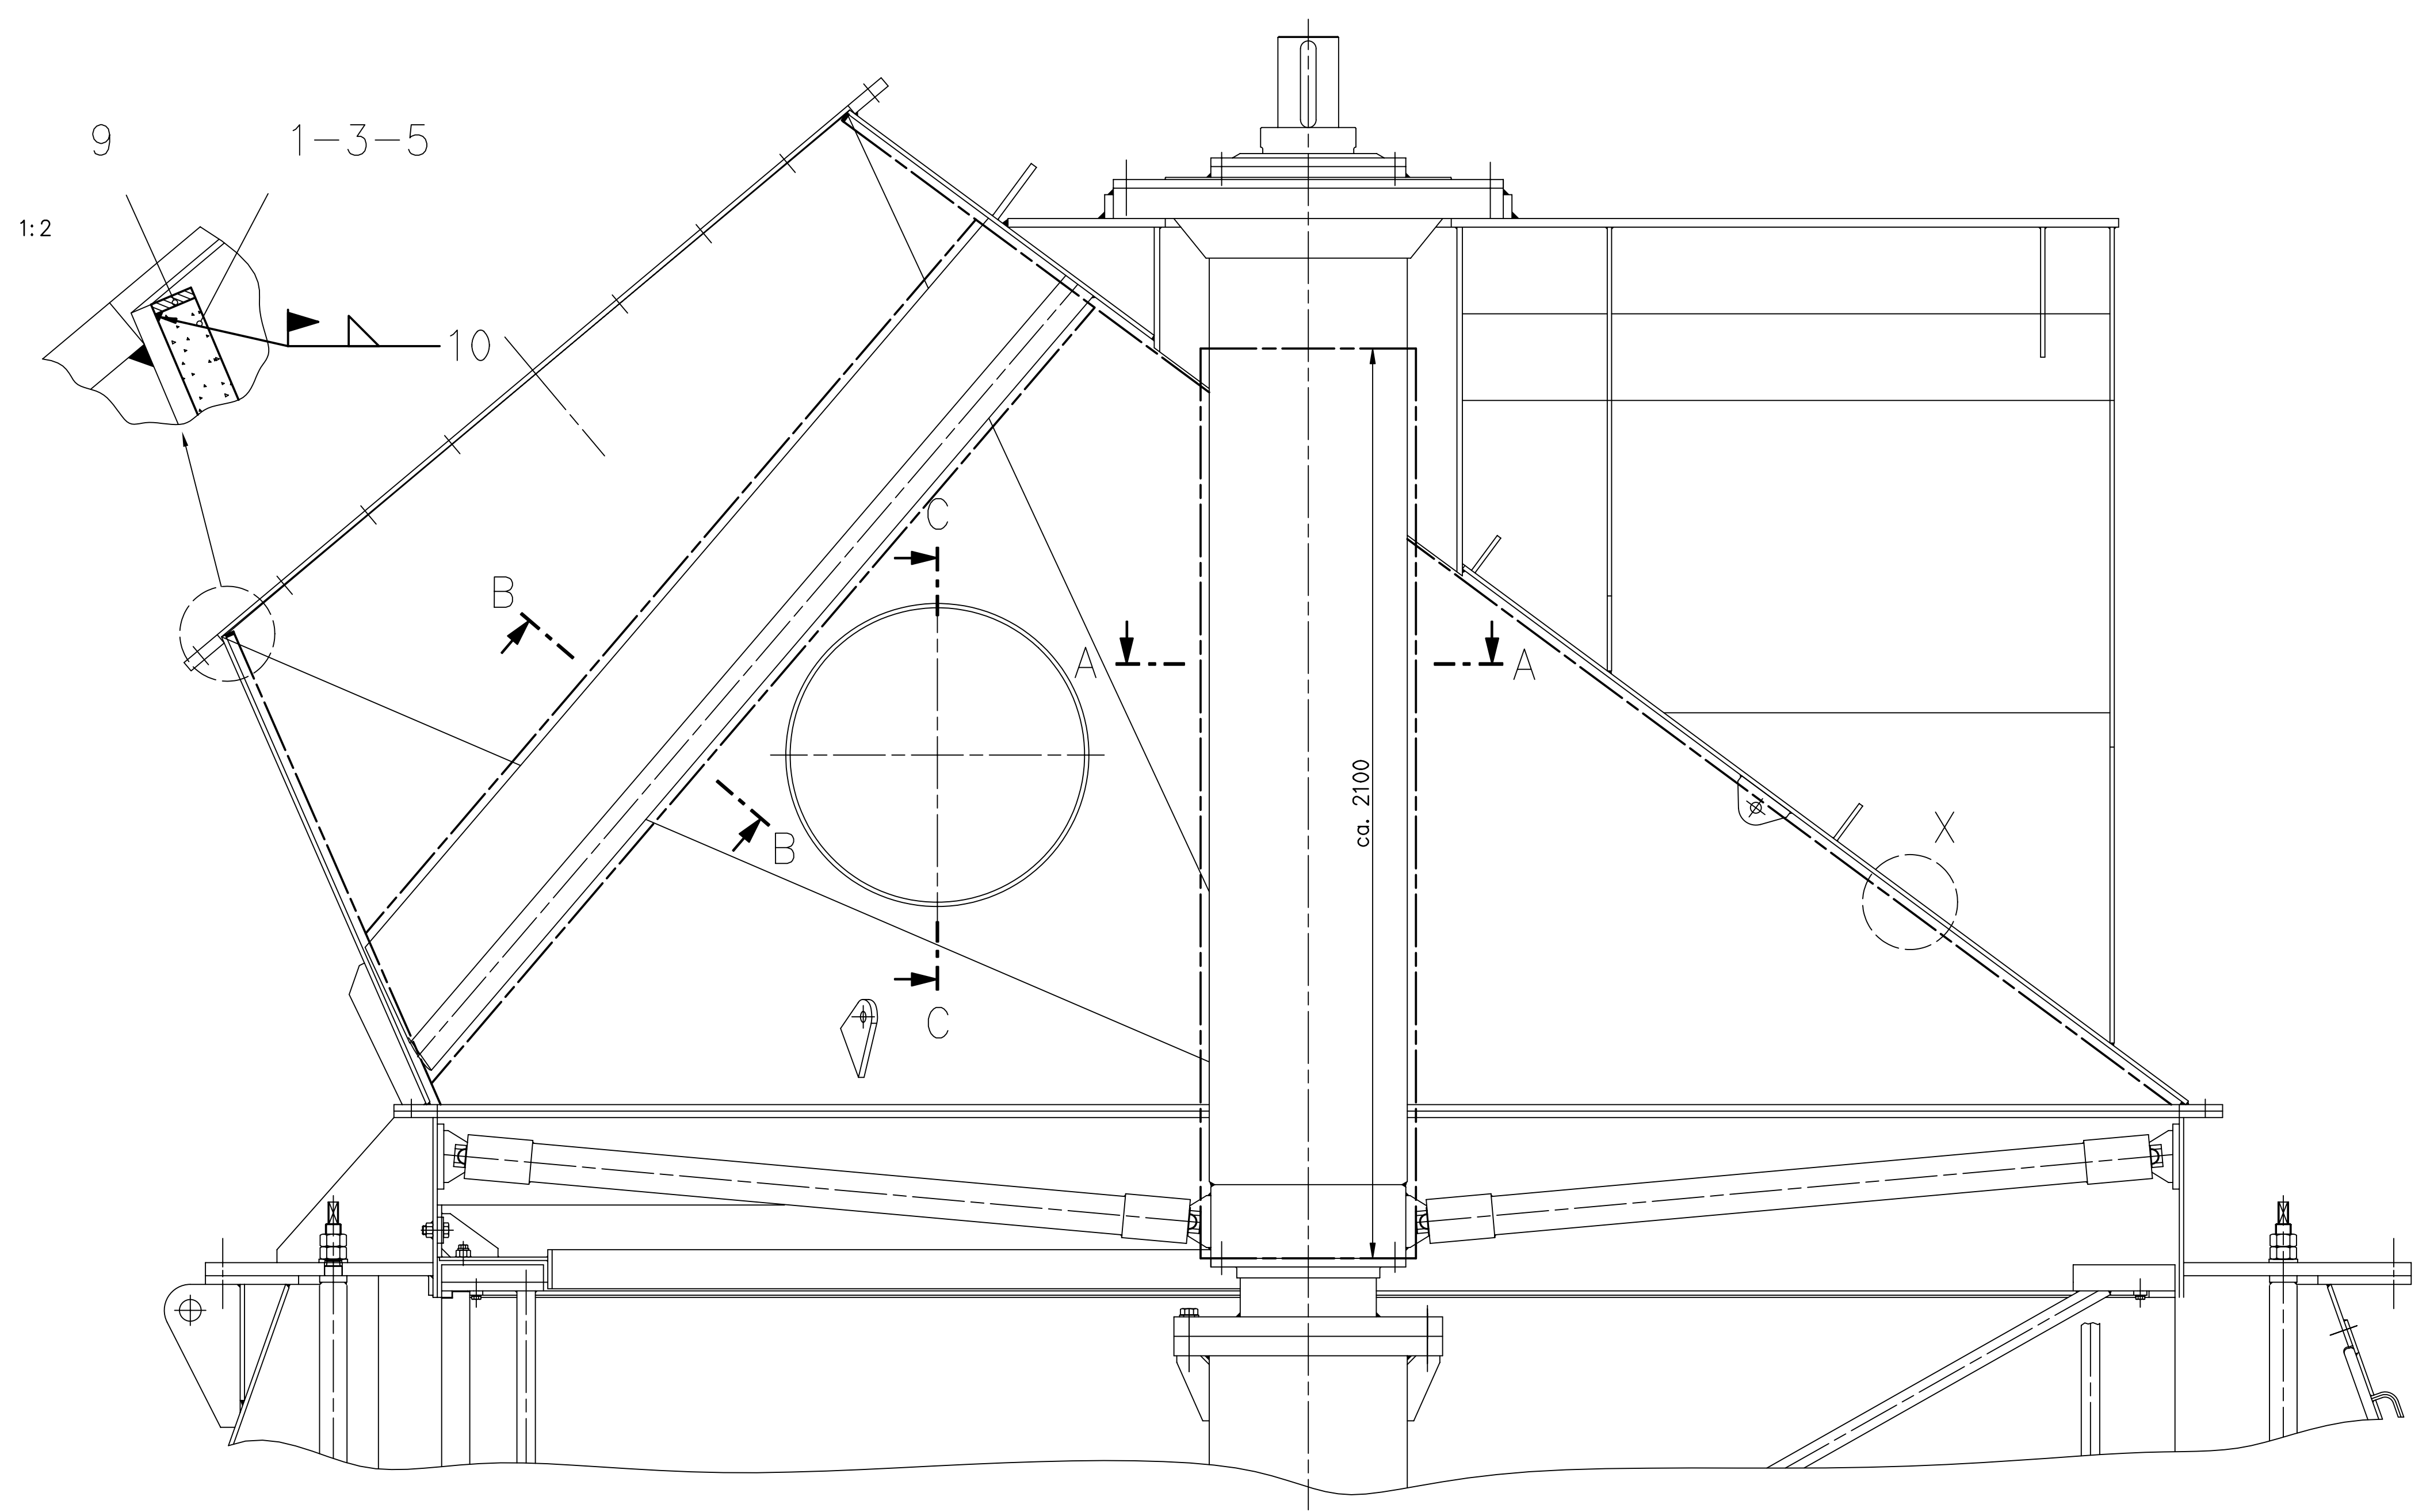


----- Panzerung t=20 ganzflächig
siehe Einzelheit X
LINING t=20 OVER COMPLETE SURFACE
SEE DETAIL X

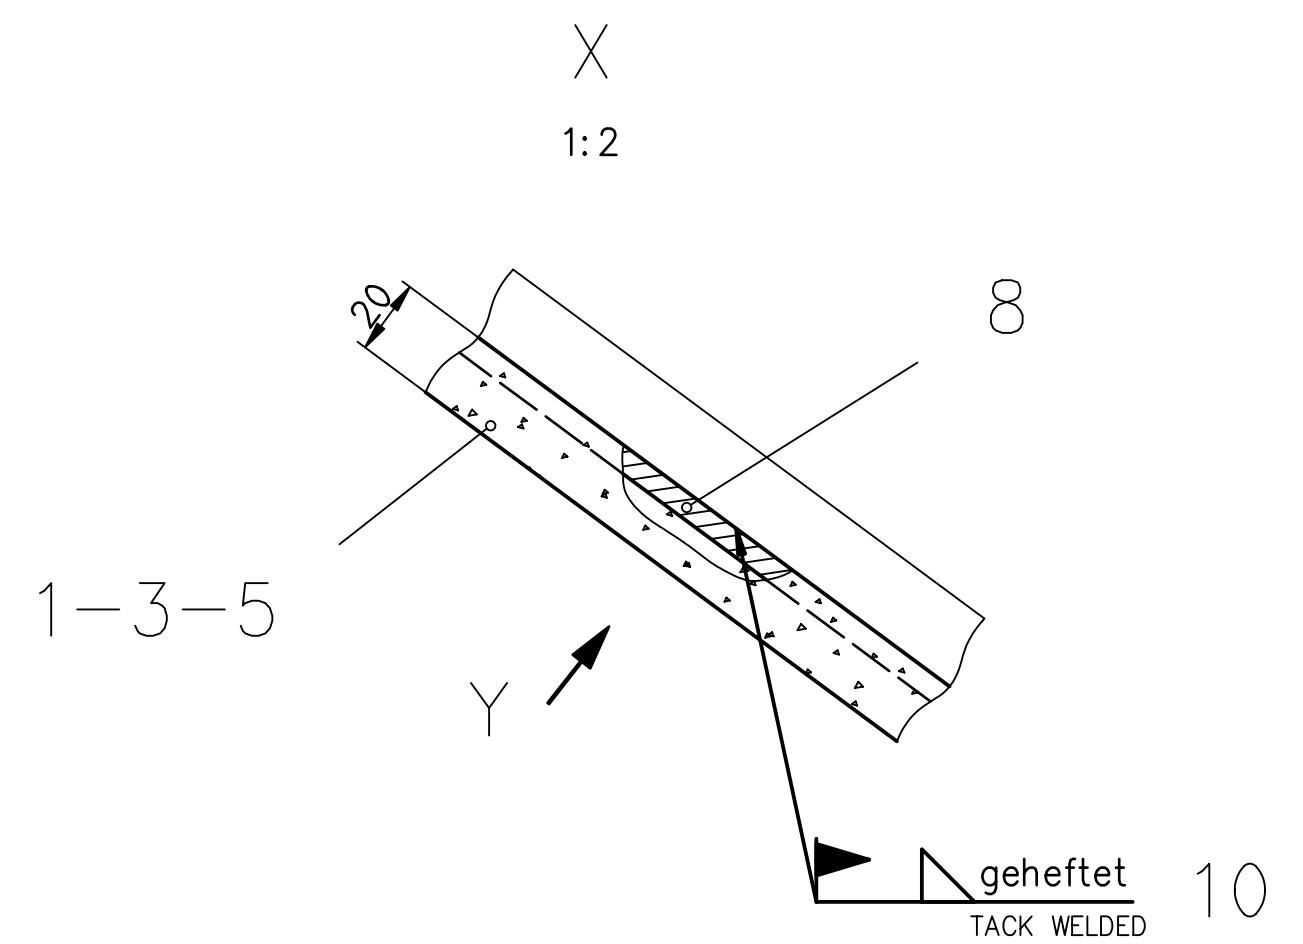

Anordnung der Heftstellen
ARRANGEMENT OF TACK WELDS

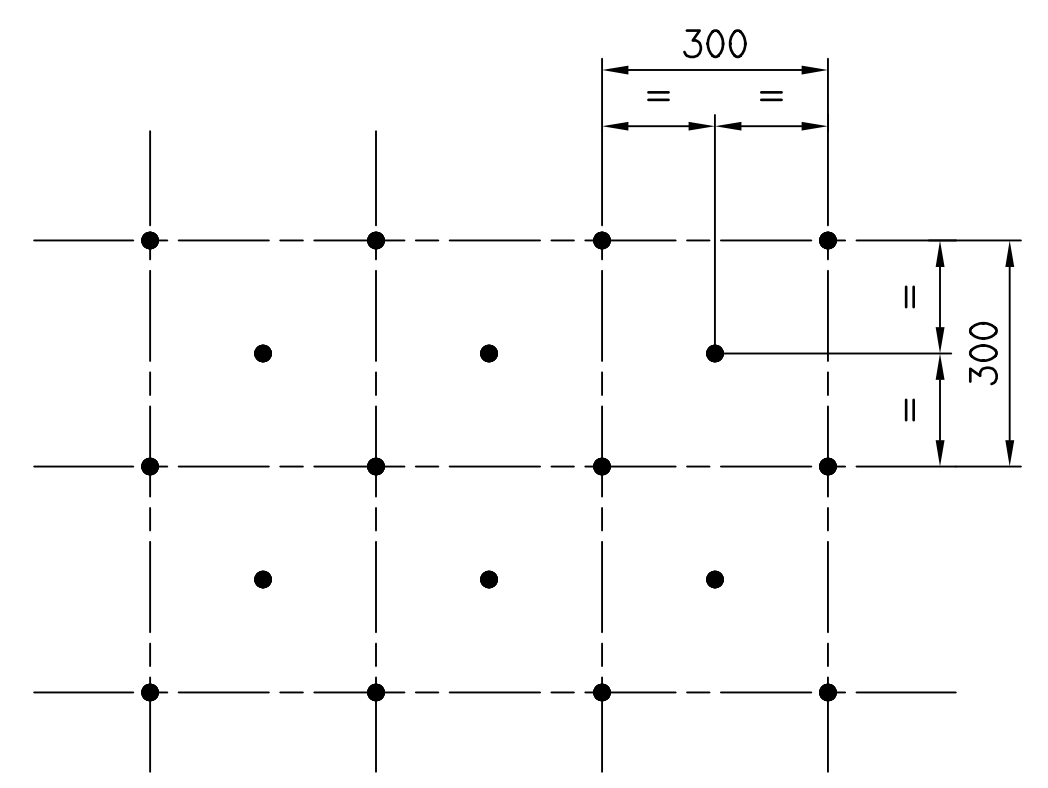


A-A

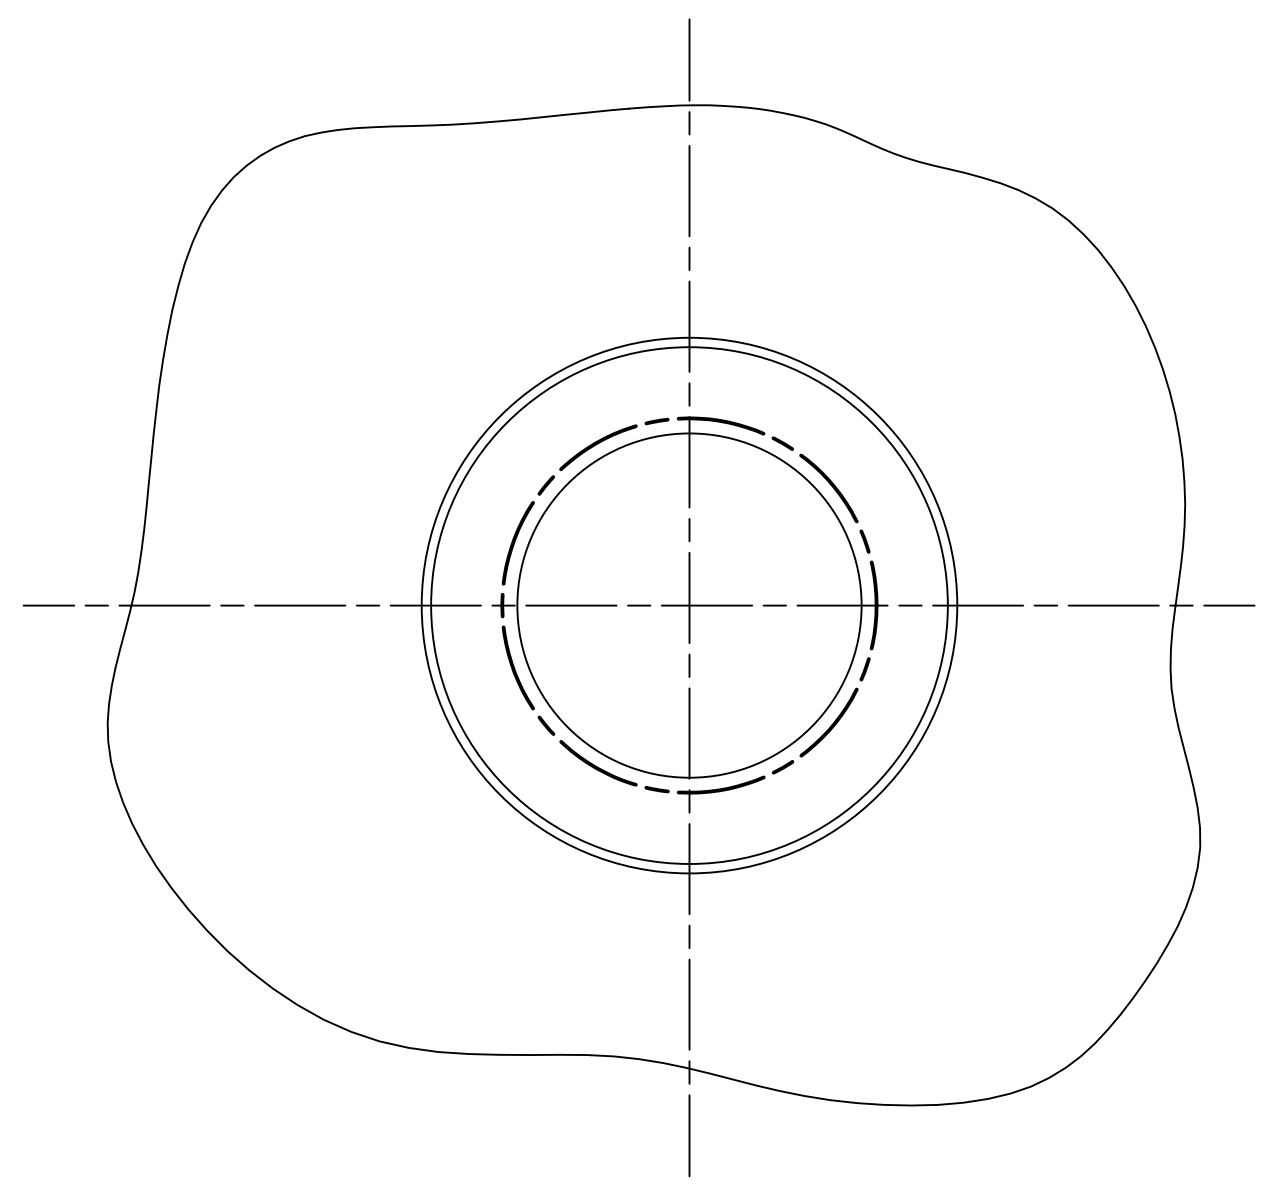


B-B

1:5

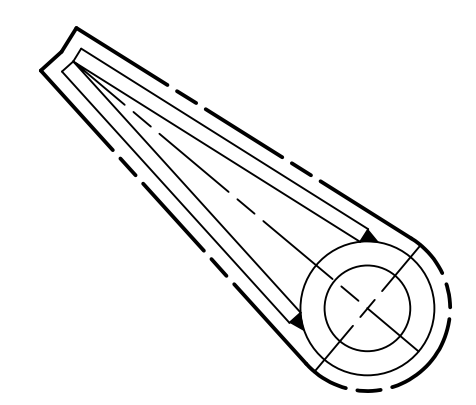

C-C

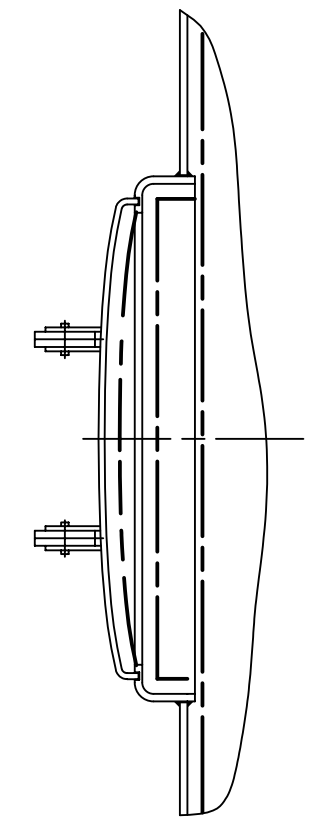

Ges.-Gew.	2250 kg	Betreff:	
Gez.	24.06.2002 fg	Ersatz für	
Gepr.	25.06.2002 SL	Entstanden aus	
File-Name: /konst/dwg/572/028598-00-1			
Plotdatum: 25.06.02			
Oberflächenzeichen		☒	☒
Mittenrauhwert R_a in μm		☒	☒
Masse ohne Toleranzangaben		☒	☒
nach DIN 7168 Gütegrad mittel		Anlieferzustand	$R_a \leq 50$
			$R_a \leq 12,5$
			$R_a \leq 3,2$
			$R_a \leq 0,8$
			$R_a \leq 0,1$
Masstab		SICHEROBERTEILPANZERUNG; KPL.	
1:10		CLASS.UPP.HOUSING LINING; CPL	
		Urheberschutz nach DIN34 vorbehalten	
		Total	BL.Nr.



CAD

028598-00-1

Äl	Anzahl	EDV	Mikro	Änderungen	Datum	Name	Gepr.