
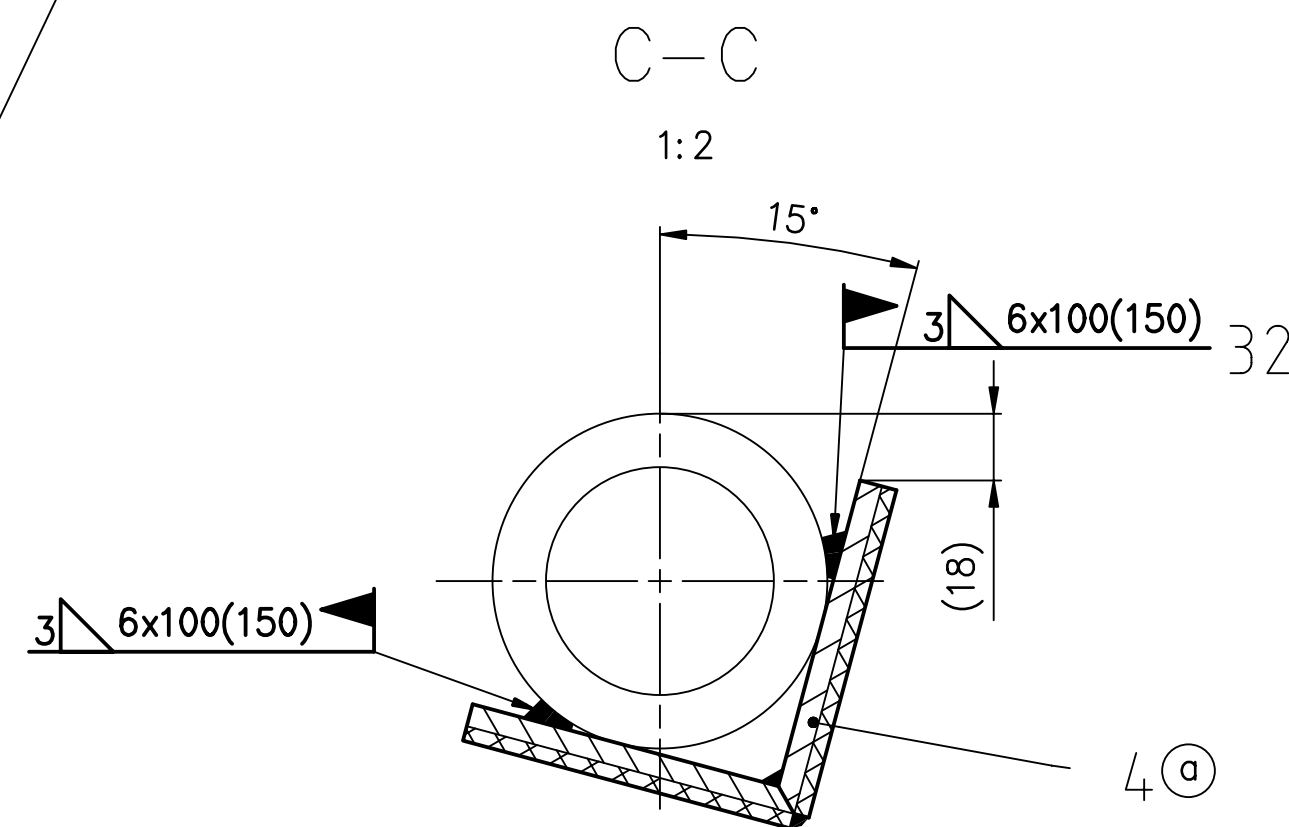
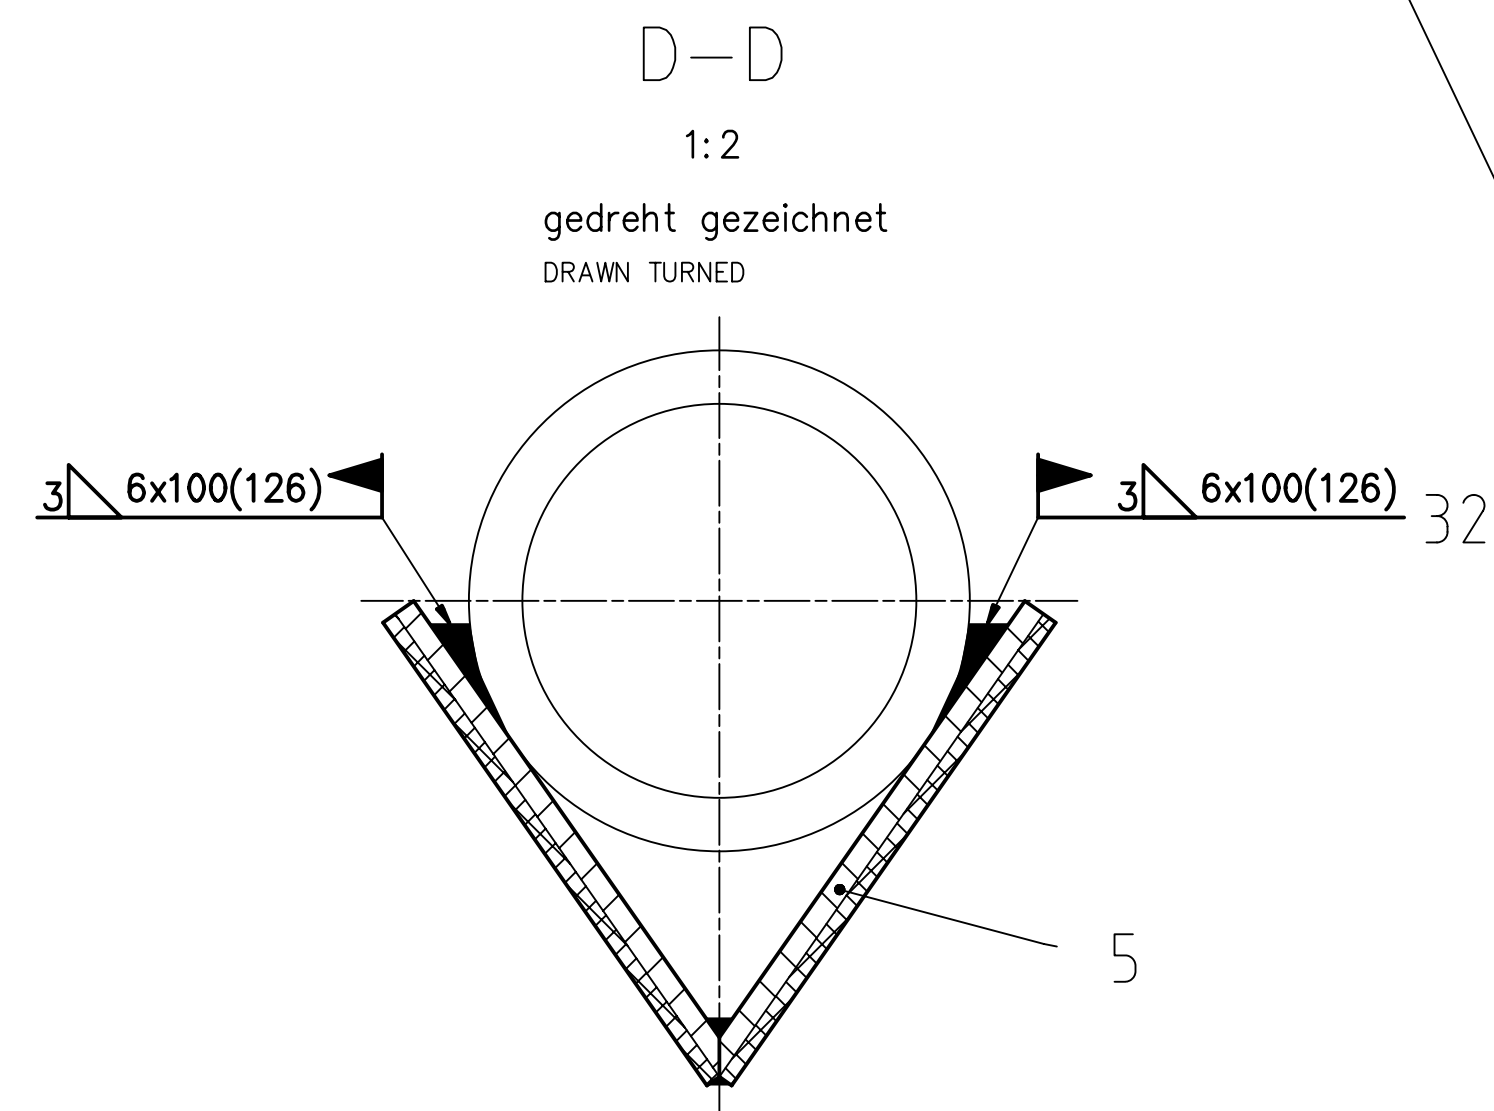
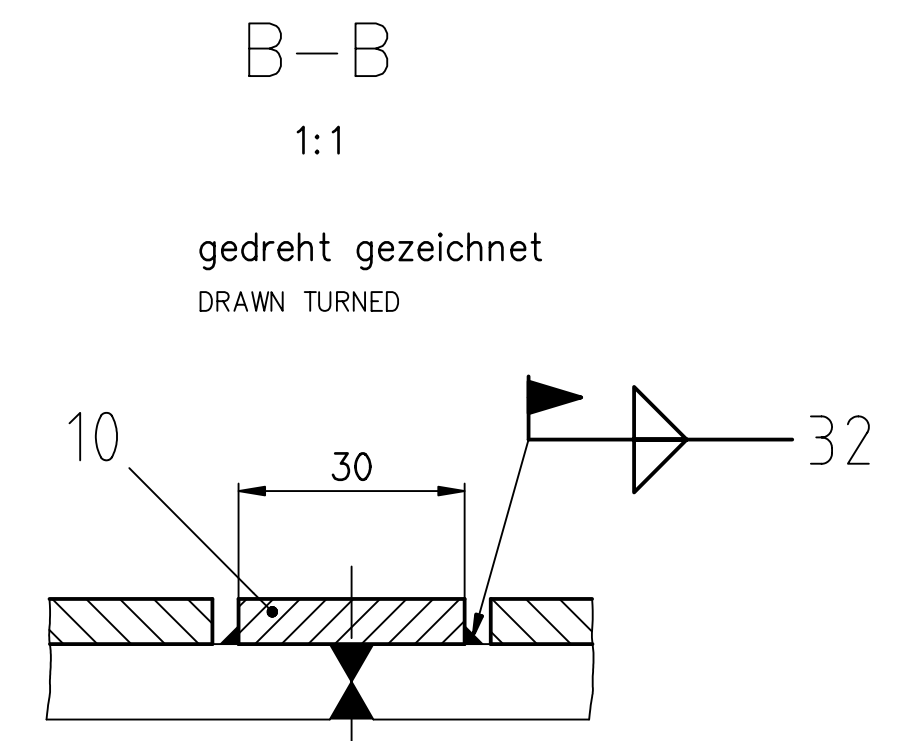
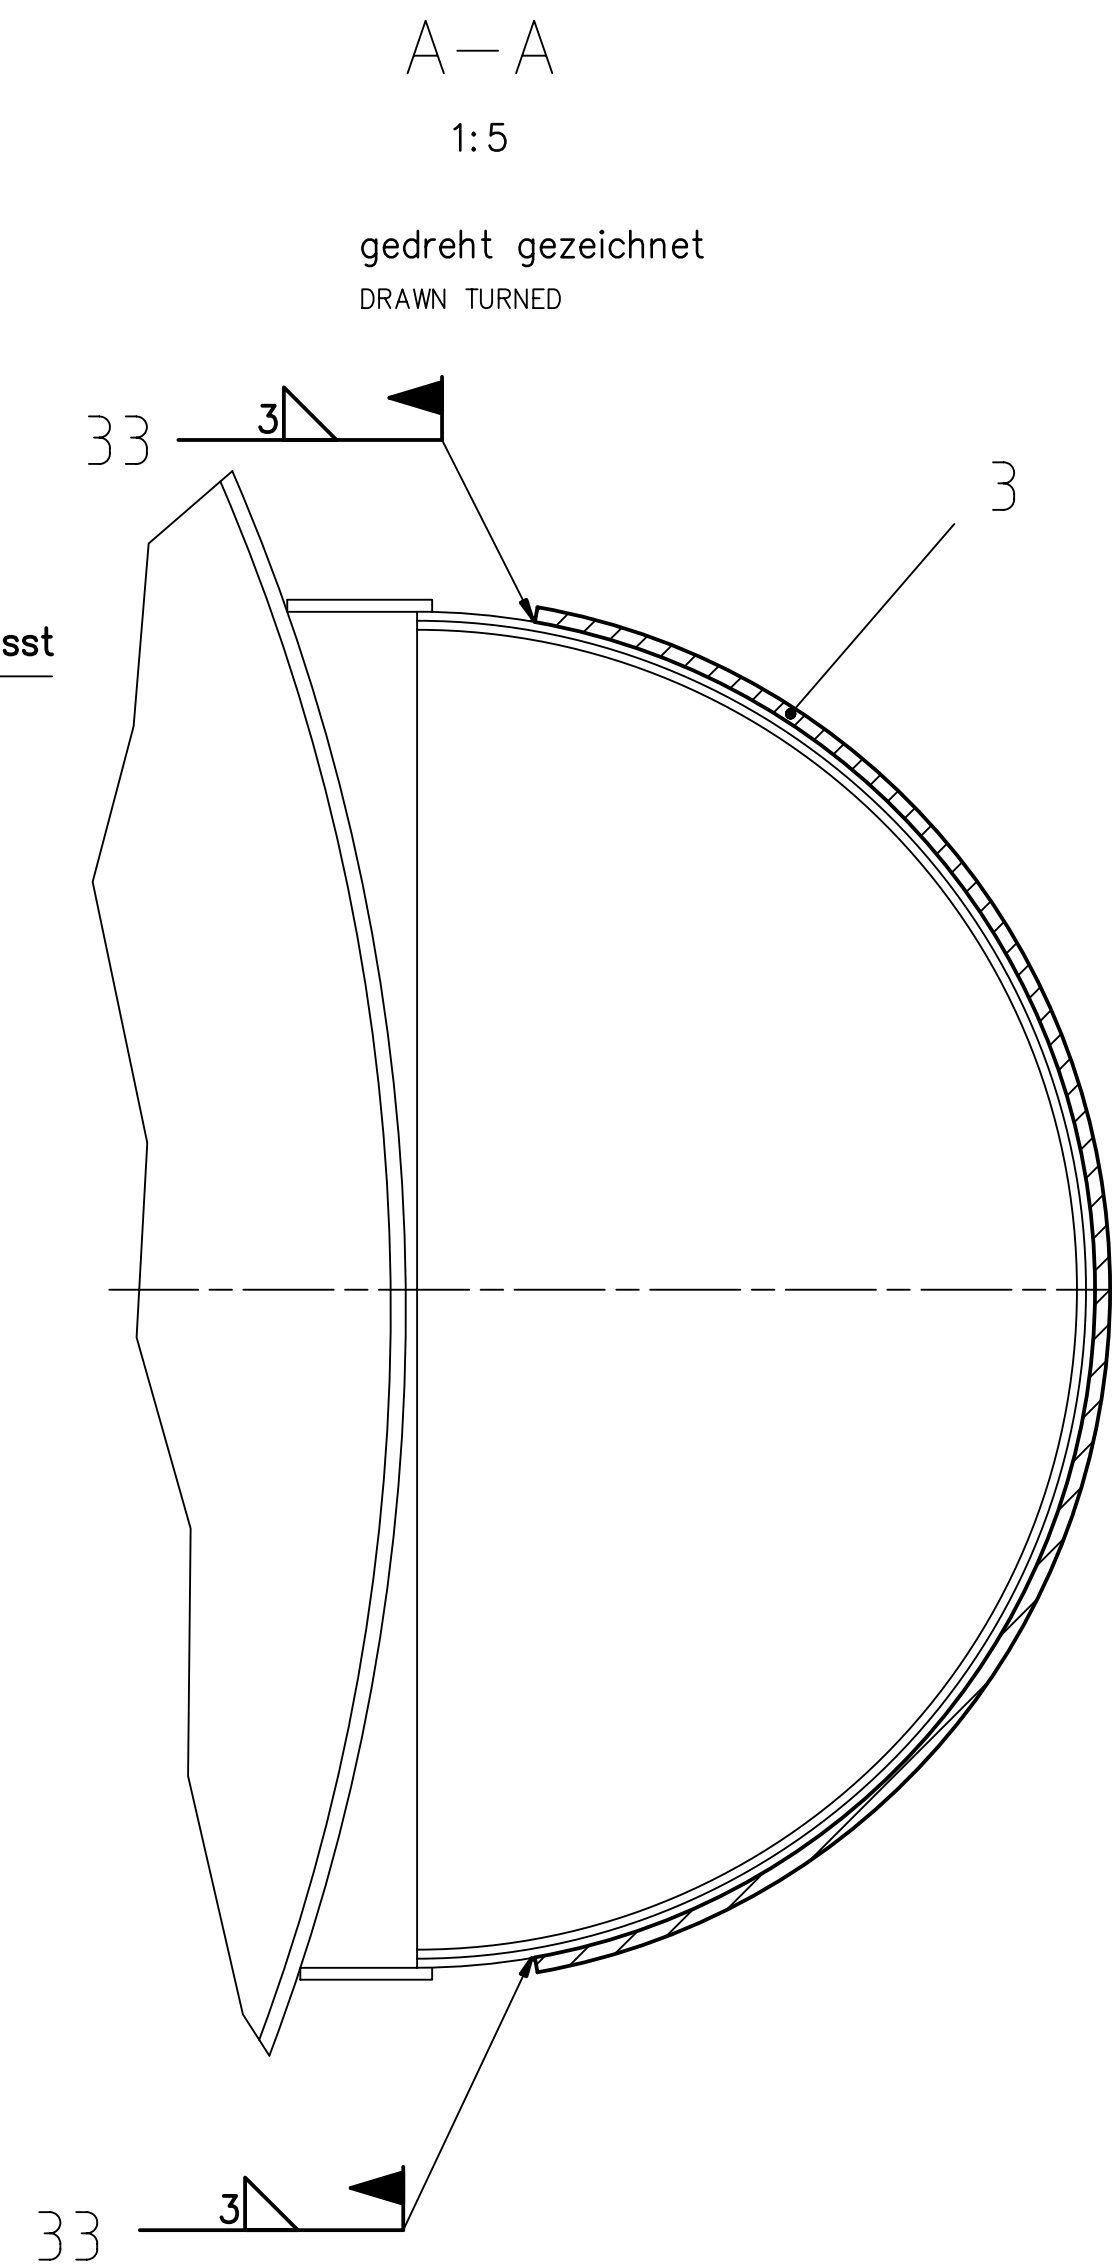
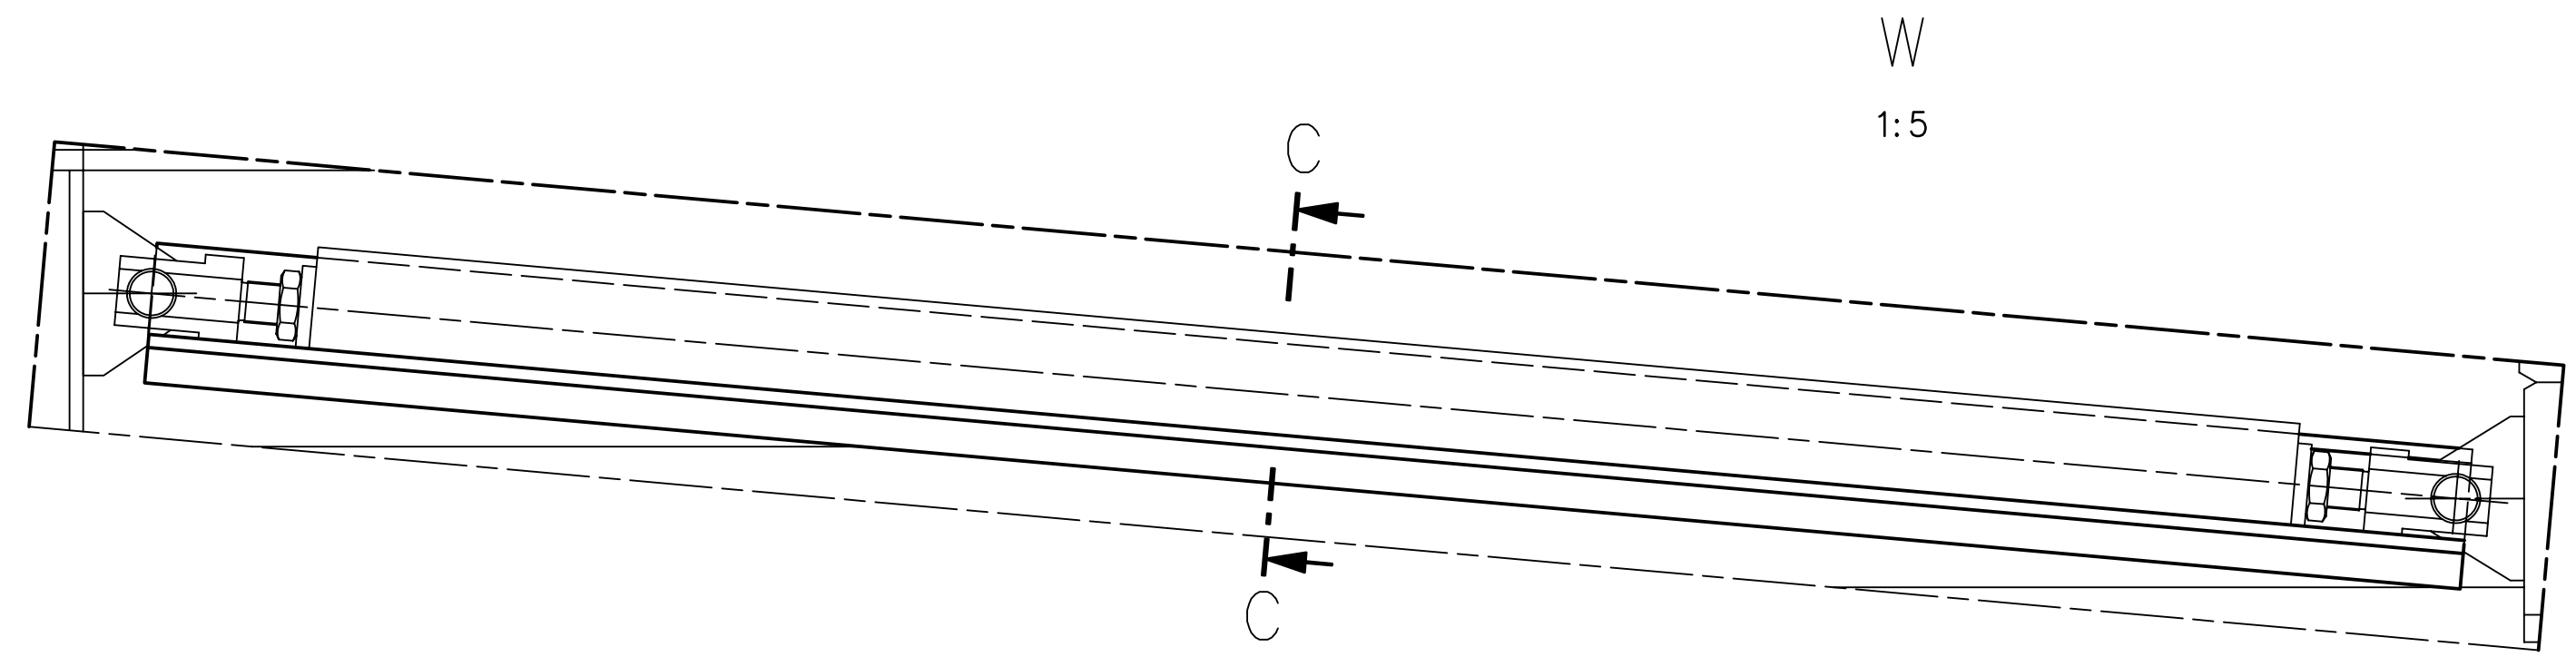


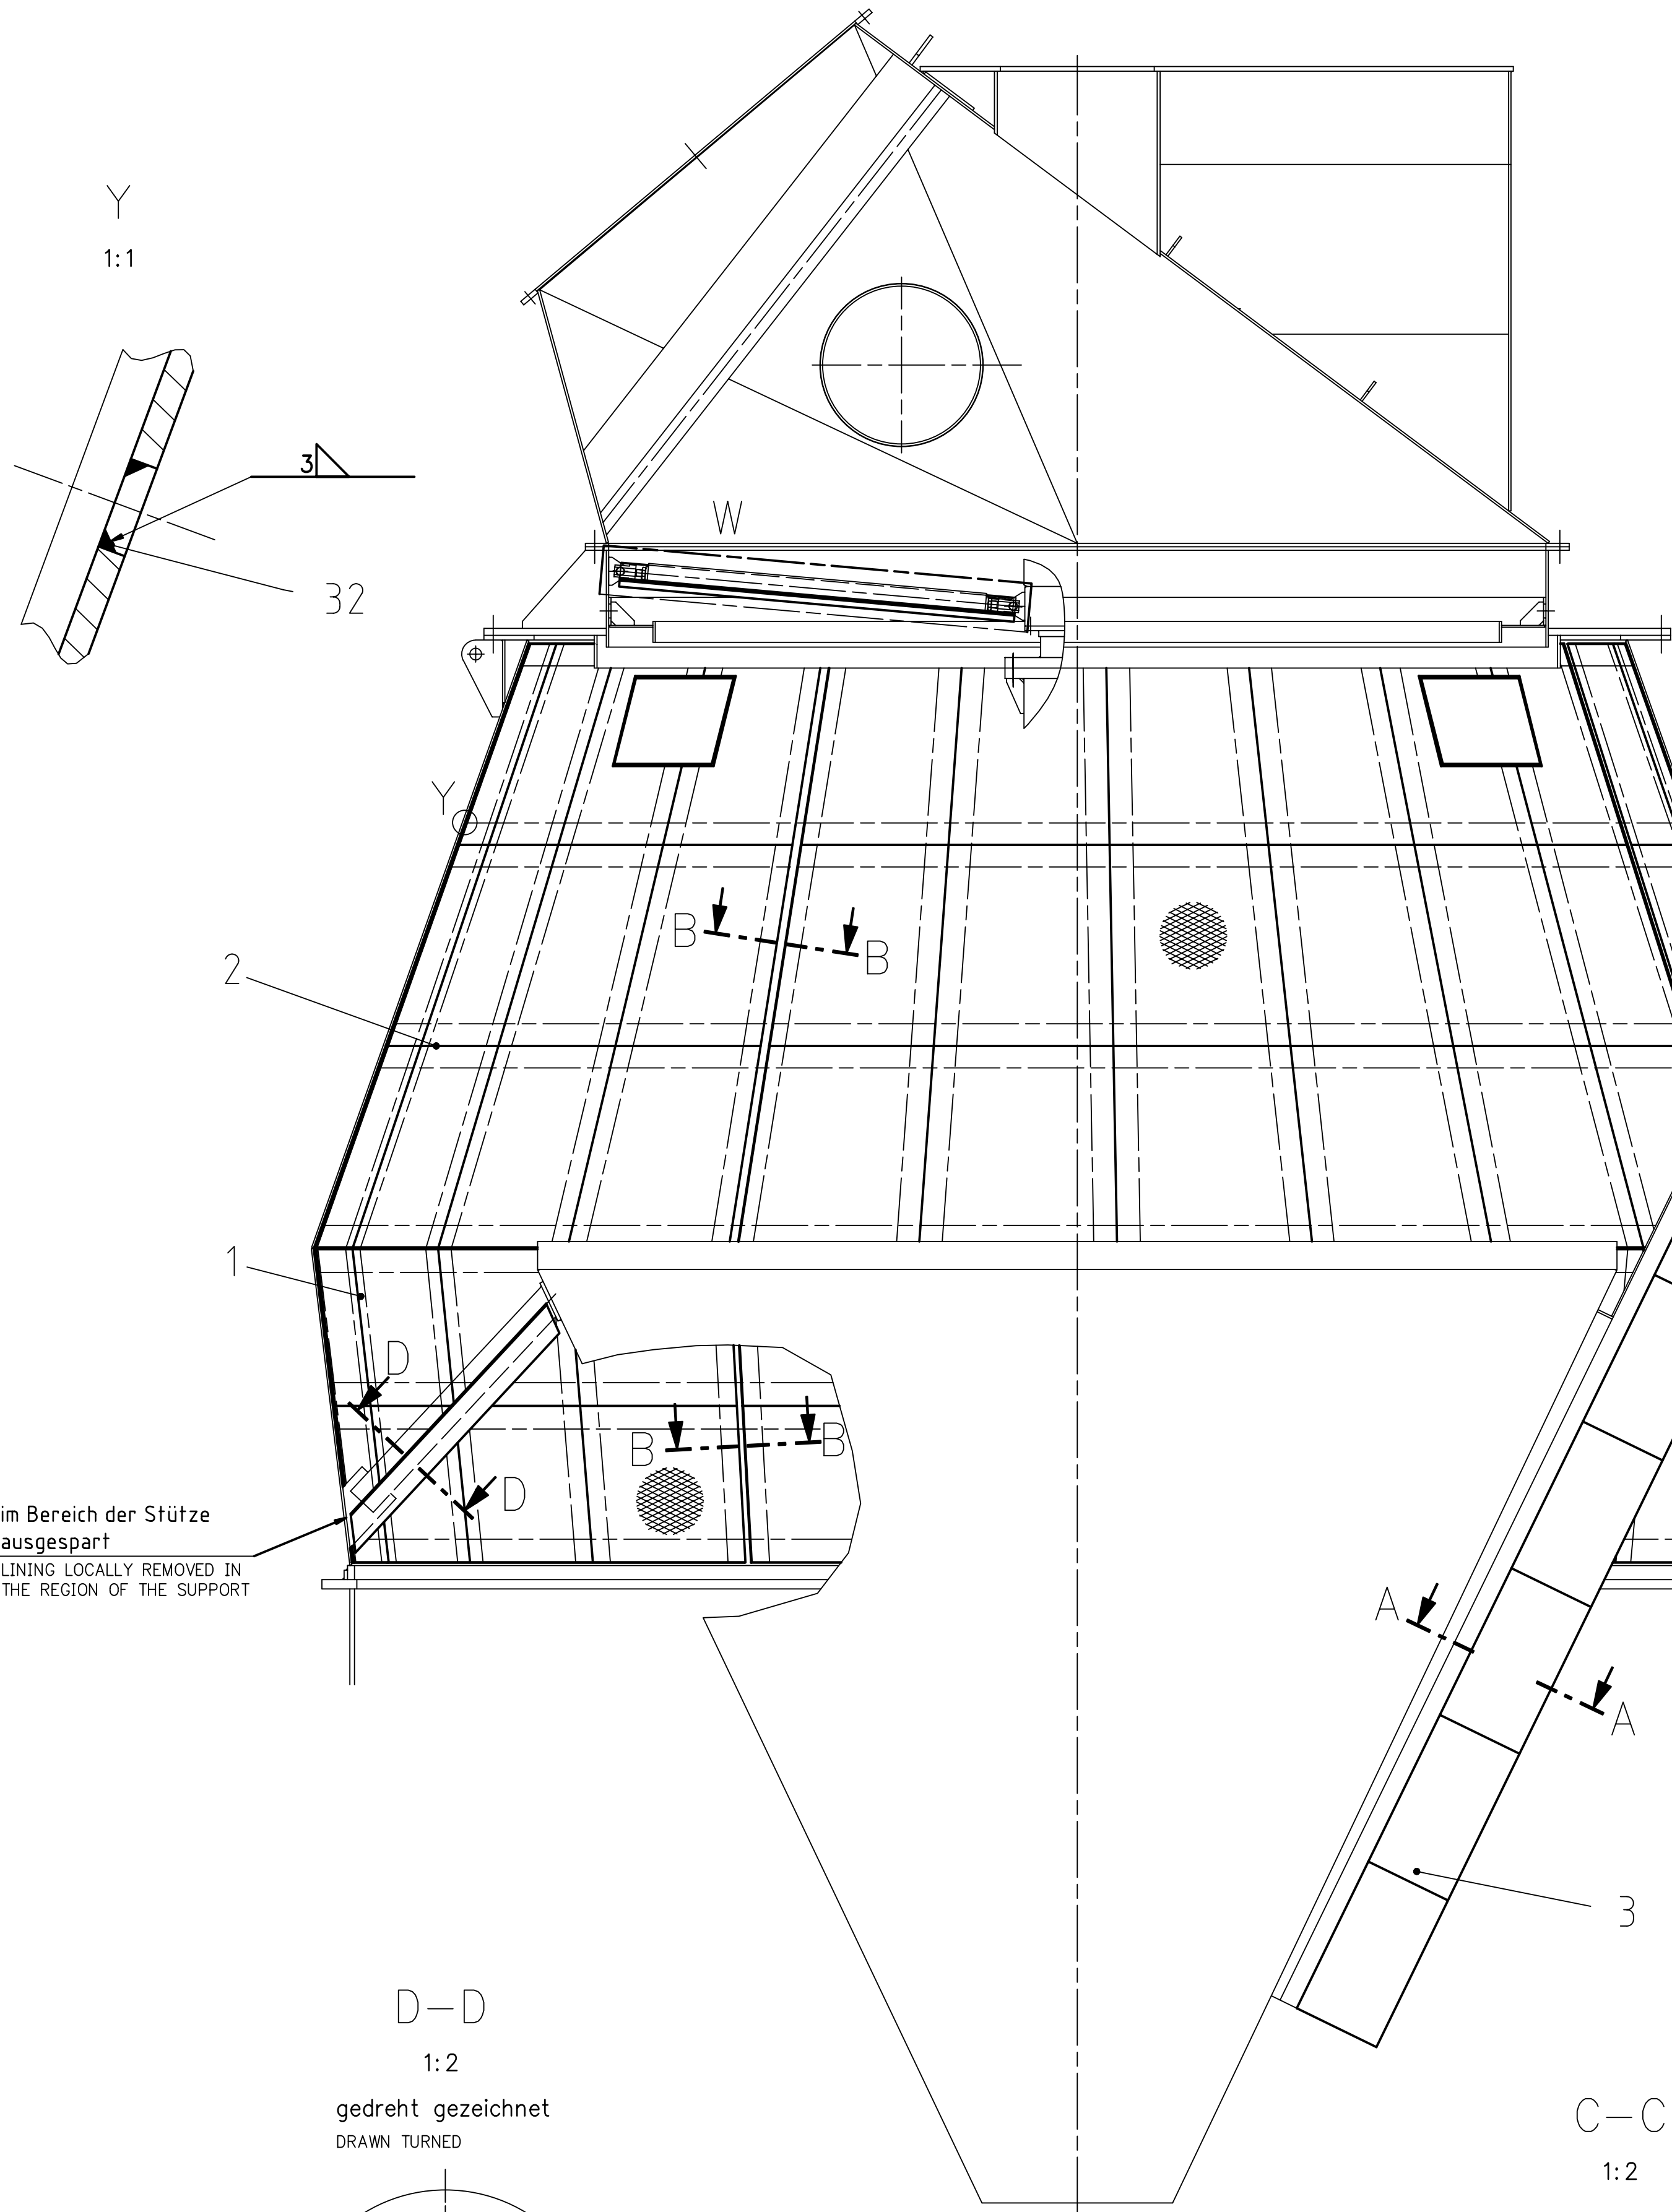

a	1	Pos.4 Abmessungen geändert	10.03.05	Fg	Zm
Ael	Anzahl	Änderungen	Datum	Name	Gepr

Allgemein Toleranzen nach GENERAL TOLERANCES ACC TO		ISO 2768 – mK			
Brennschneite nach FLAMECUTS ACC TO		ISO 9013 – 332			
Schweißkonstruktion nach WELED CONSTRUCTION ACC TO		ISO 13920 – B			
Schweißnahtvorbereitung EDGE PREPARATION FOR WELDING ACC TO		DIN EN ISO 9692-1			
Schmelzschweißverbindung nach ÜBUNGEN WELED ACC TO		ISO 5817 – C			
Oberflächenzeichen SURFACE FINISH MARK R _a ≤ [µm]		ISO 1302			
					
		Roh RAW	50	12,5	3,2
				0,8	0,1
Werkstückkanten nach COMPONENT EDGES ACC TO		ISO 13715		 	
Maßstab SCALE 1:20		SICHTERPANZERUNG; KPL. LSKS 66 CS CLASSIFIER LINING; CPL.		Gezeichnet DRAWN 24.03.2004 Fg Geprüft CHECKED 06.04.2004 Zm	
		028725-00-1		Made in DIMENSIONS IN mm Darstellungsmethode PROJECTION METHOD ISO 128 Datum / DATE Name / NAME	
m pr.		Total / TOTAL		Bl. / SHT. Bl.Nr. / SHT.NO.	