



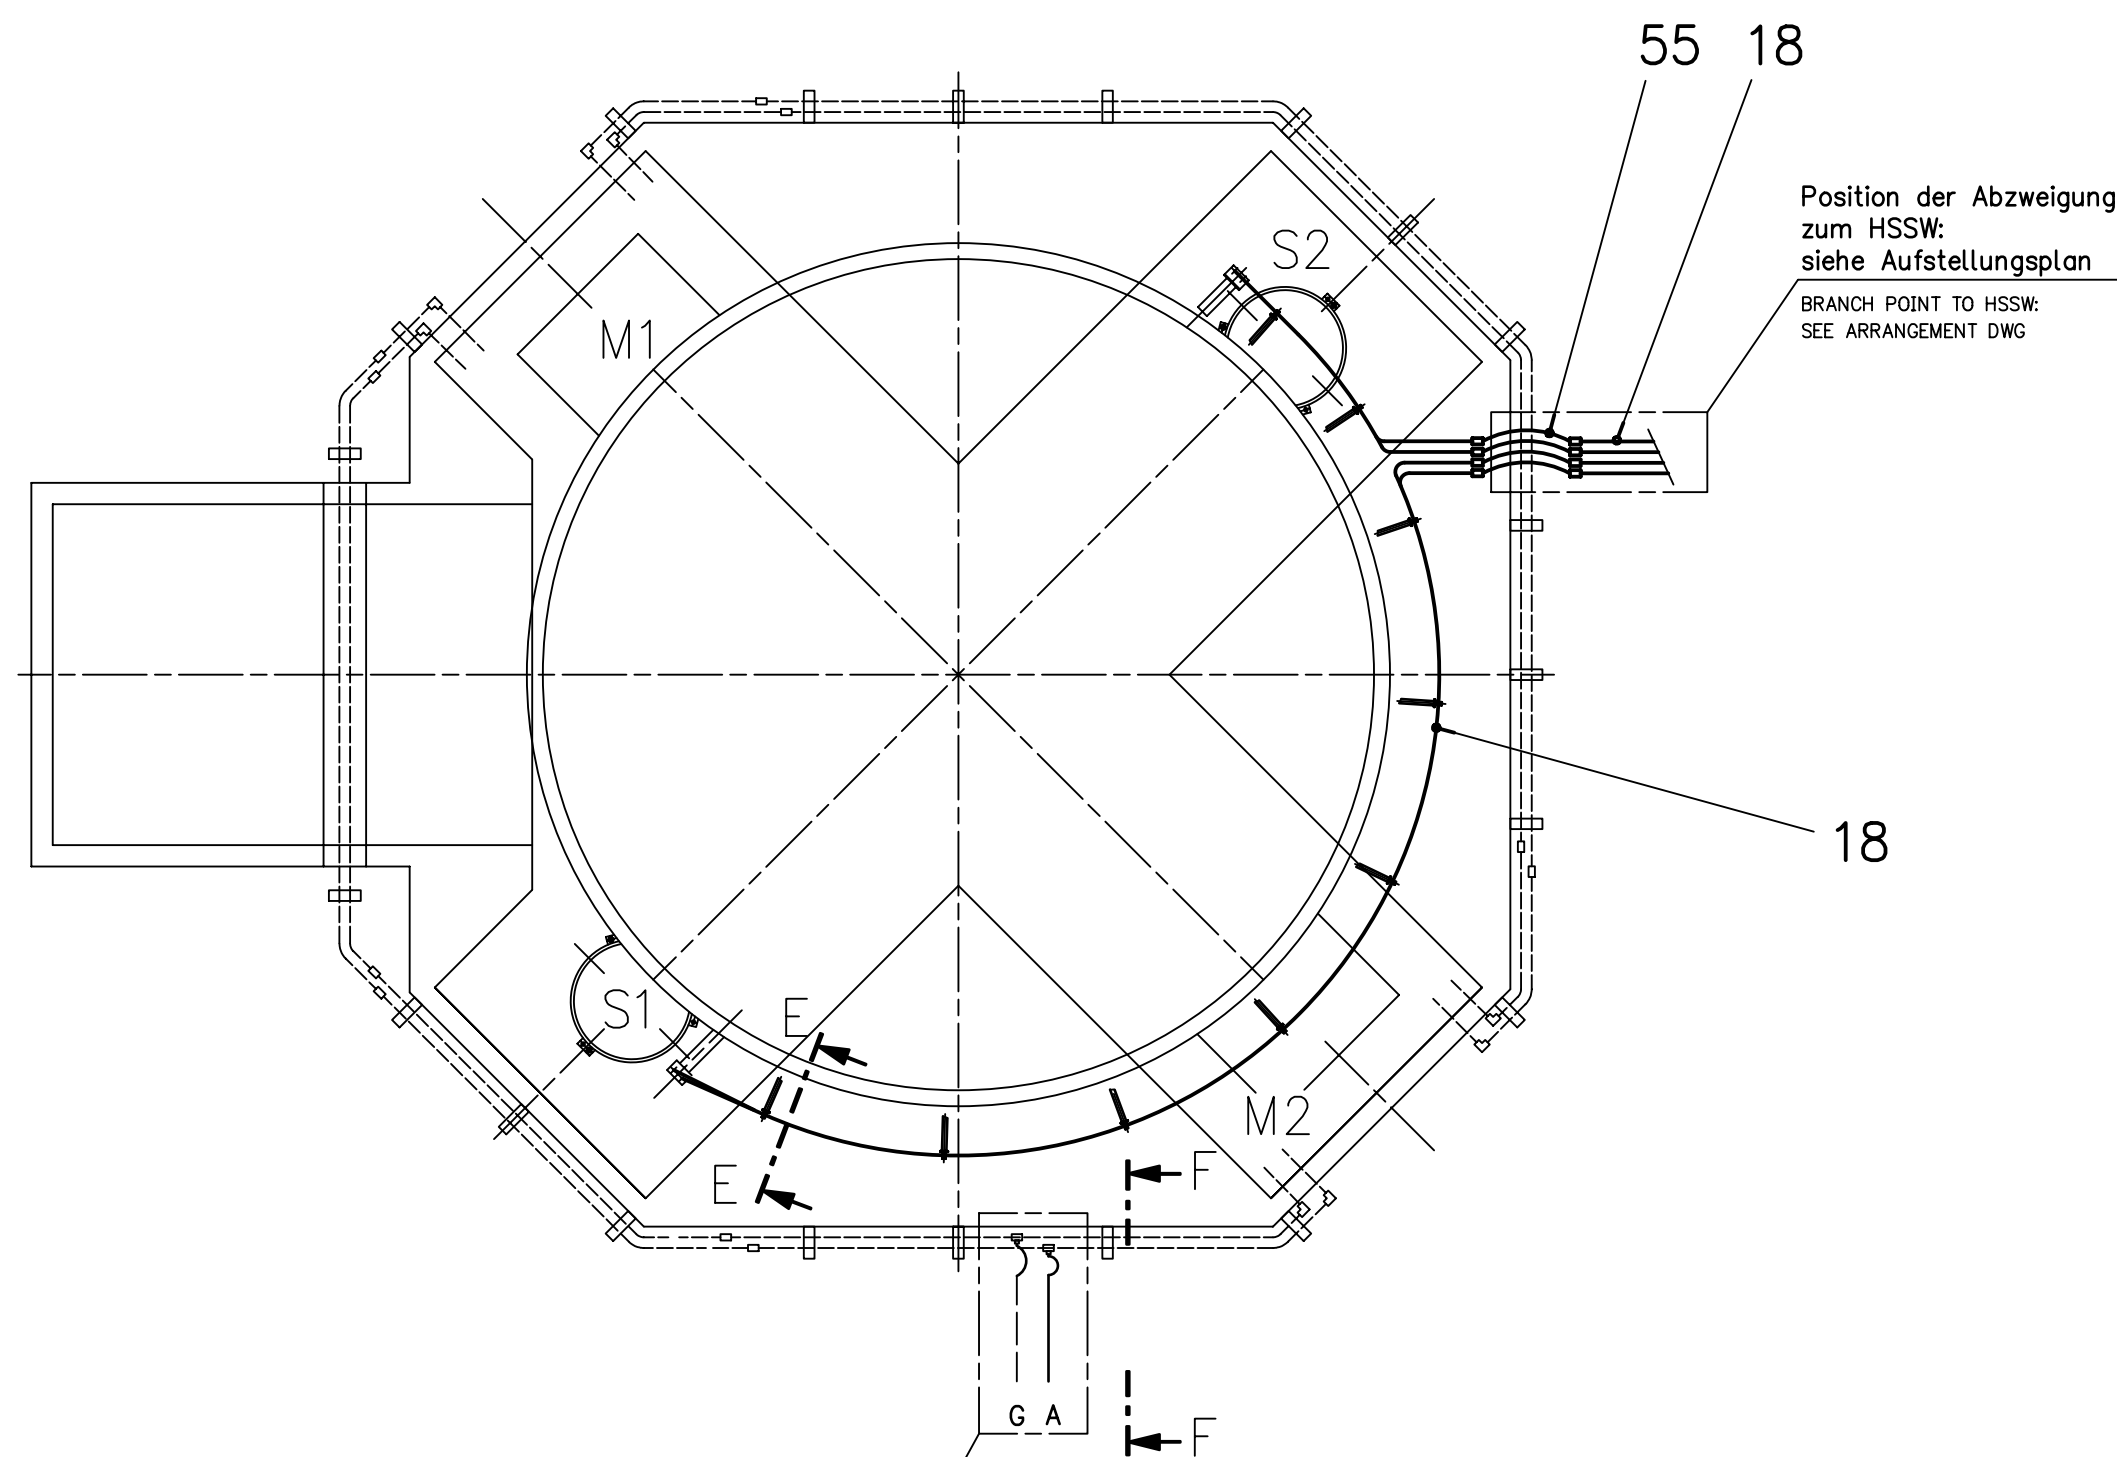


Position der Abzweigung zum HSLM: siehe Aufstellungsplan
BRANCH POINT TO HSLM: SEE ARRANGEMENT DWG



Position der Abzweigung zum HSSW: siehe Aufstellungsplan
BRANCH POINT TO HSSW: SEE ARRANGEMENT DWG

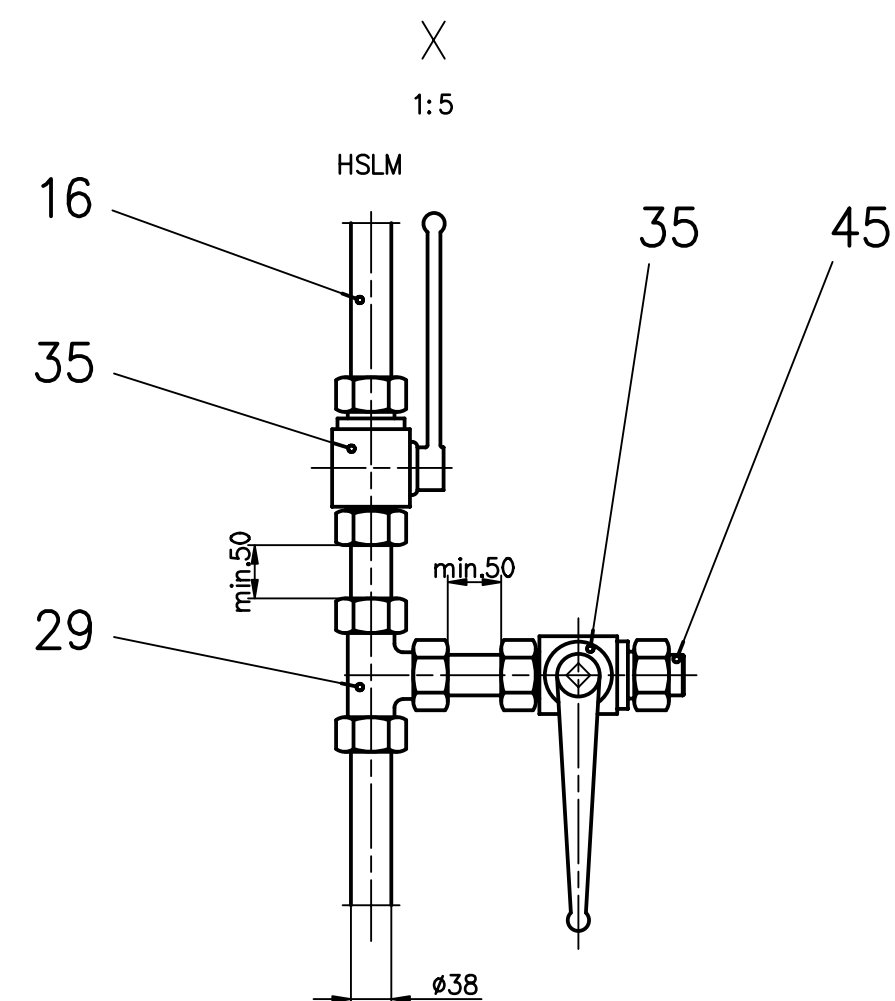



Ringleitung
RING PIPELINE

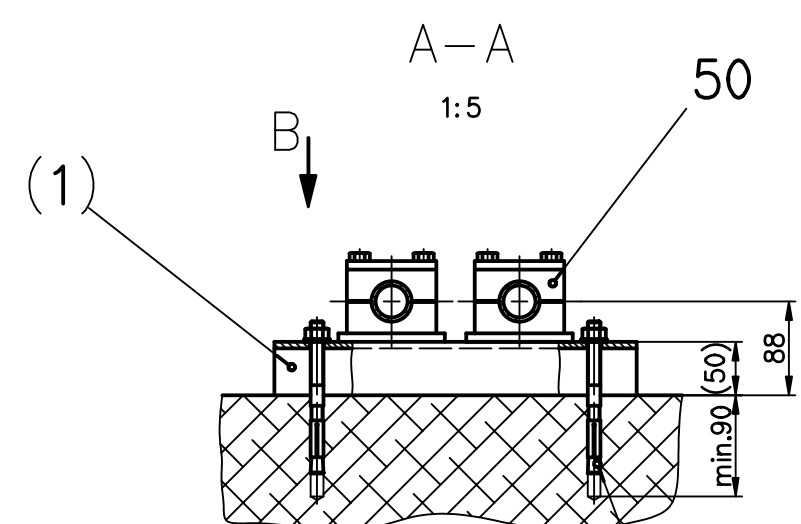



B
1:5

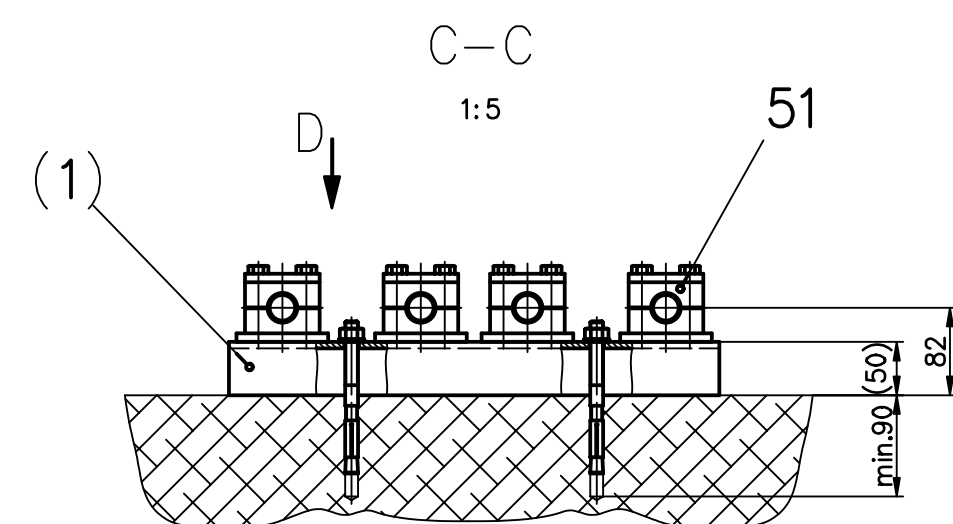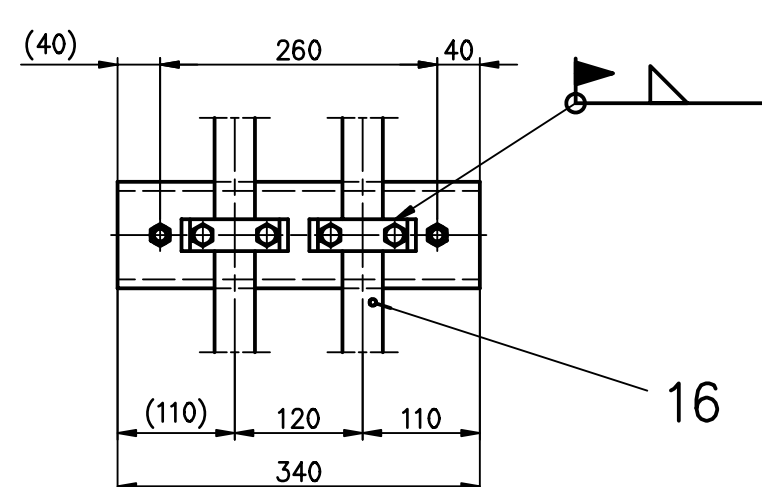


D
1:5

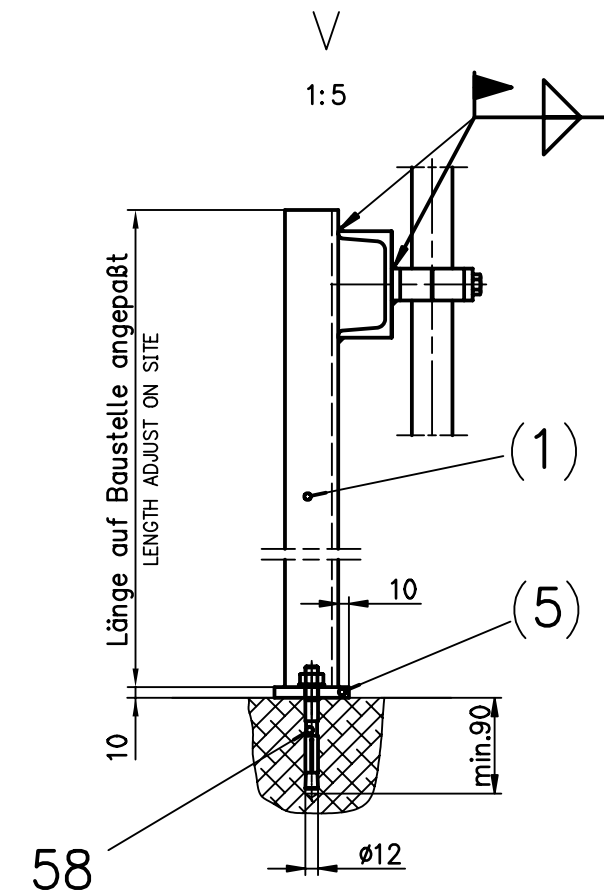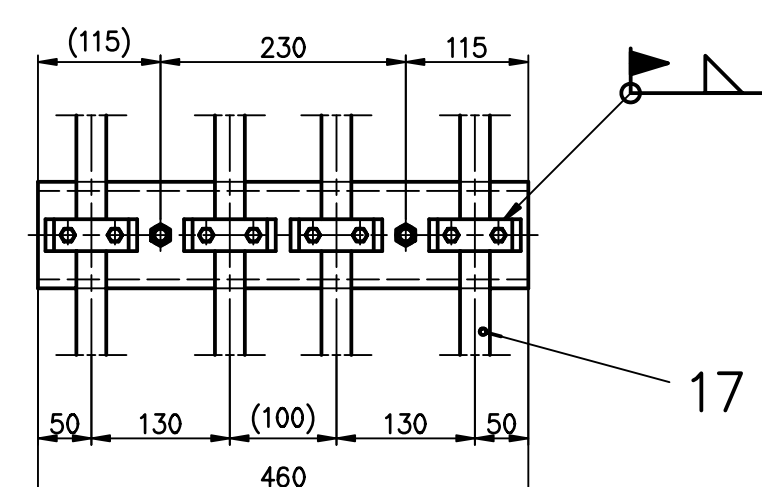


4
1:5

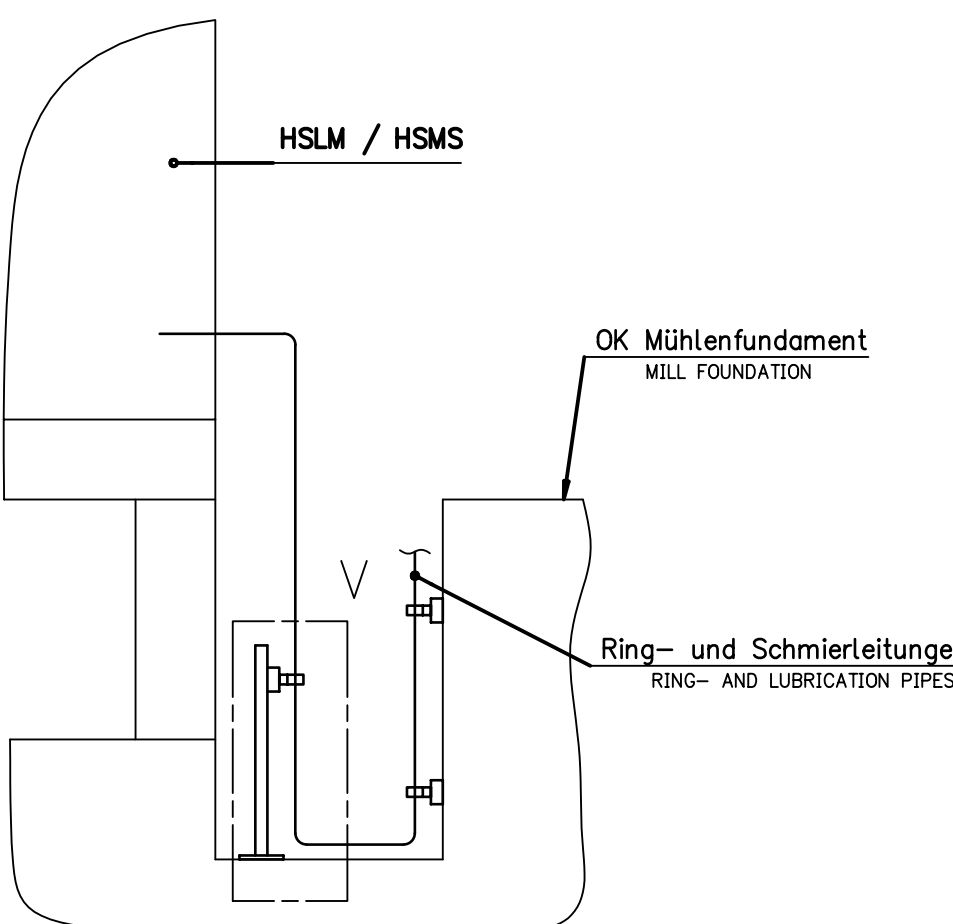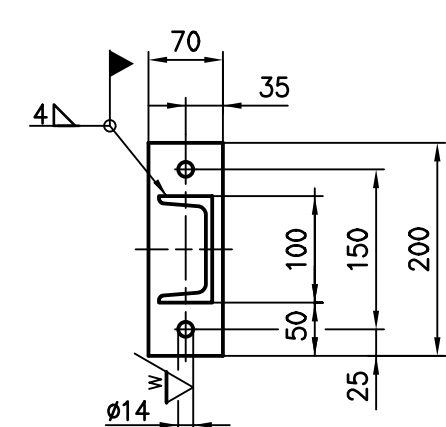

F-F
%

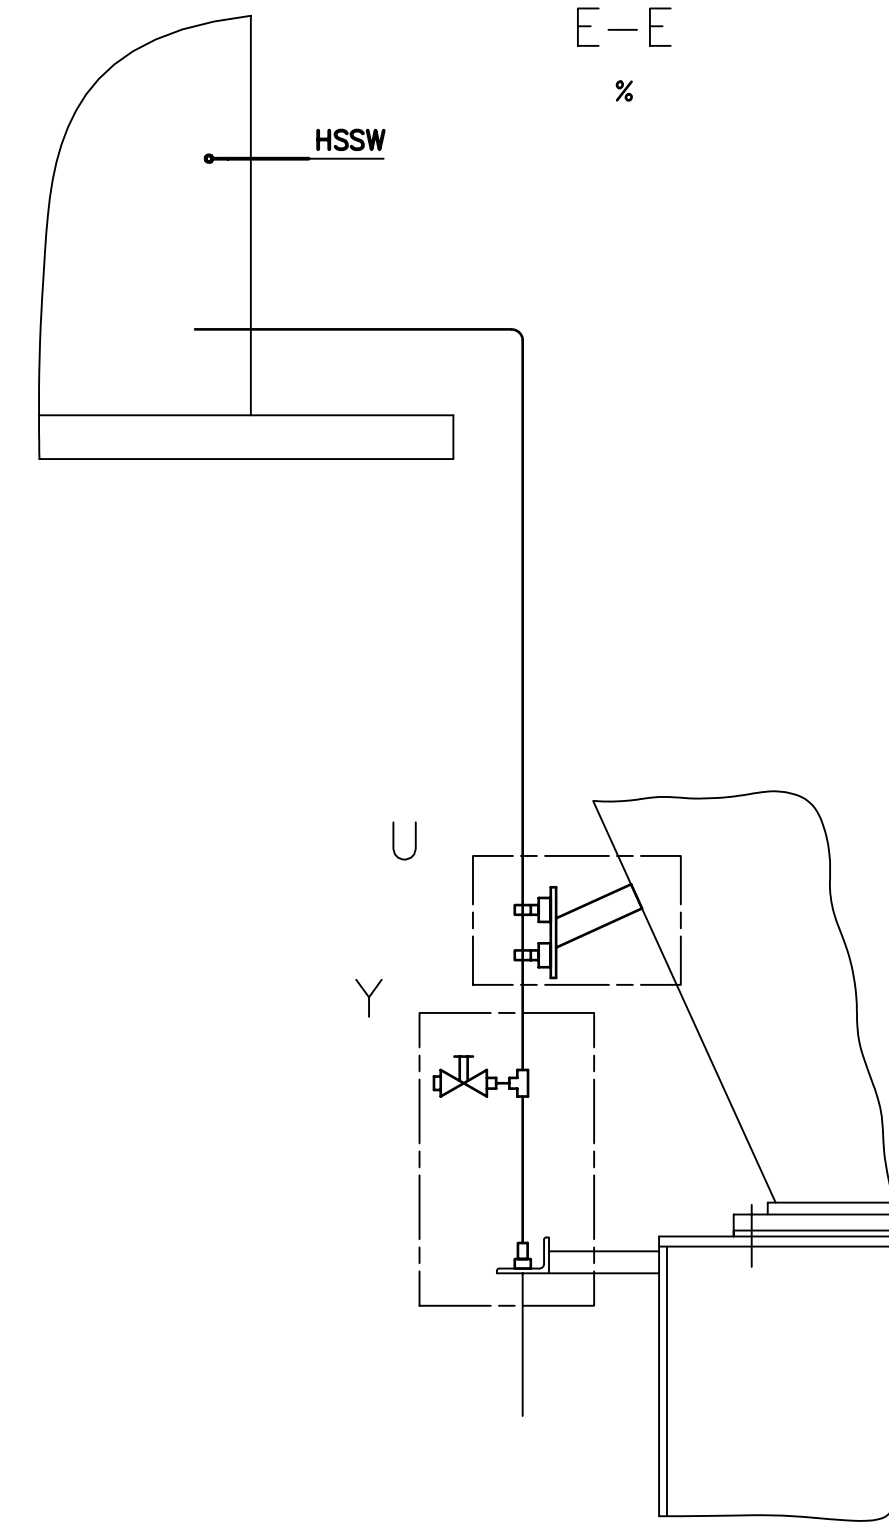

E-E
%

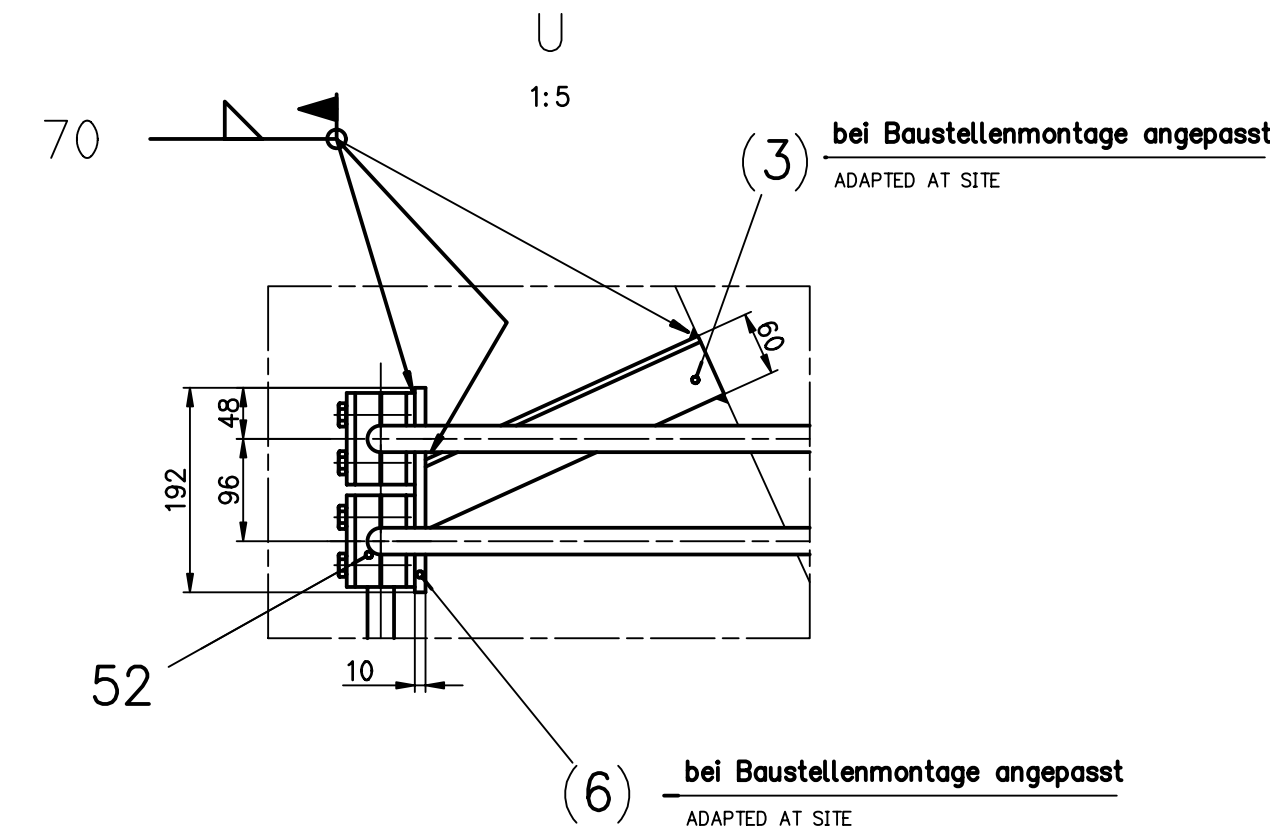

U
1:5

HSSW
A1,A2-Arbeitsdruck
OPERATING PRESSURE
G1,G2-Walzen heben/senken
ROLLERS LIFT/LOWER

HSLM
A-Arbeitsdruck
OPERATING PRESSURE
G-Walzen heben/senken
ROLLERS LIFT/LOWER
HSMS
I } Mahlwälzensmierung/Druckleitung
K } ROLLER LUBRICATION PRESSURE PIPE
H } Mahlwälzensmierung/Saugleitung
J } ROLLER LUBRICATION SUCTION PIPE

Rohrleitungen für Montage einer Begleitheizung vorbereitet
PIPE LINES PREPARE FOR INSTALLATION OF TRACE HEAT

Hinweise für Baustellenmontage
NOTE FOR SITE ASSEMBLY
Rohre 38x4 kalt gebogen, min. Biegeradius = 120 mm
Max. Abstand zwischen 2 Rohrschellen = 2000 mm.
Rohre 28x2 kalt gebogen, min. Biegeradius = 90 mm
Max. Abstand zwischen 2 Rohrschellen = 1500 mm.
Rohre 25x2 kalt gebogen, min. Biegeradius = 75 mm
Max. Abstand zwischen 2 Rohrschellen = 1500 mm.
Max. 3 Bögen pro Rohrstück
PIPES 38x4 COLD BENT, MIN. BENDING RADIUS = 120 mm
MAX. DISTANCE BETWEEN 2 PIPE CLAMPS = 2000 mm
PIPES 28x2 COLD BENT, MIN. BENDING RADIUS = 90 mm
MAX. DISTANCE BETWEEN 2 PIPE CLAMPS = 1500 mm
PIPES 25x2 COLD BENT, MIN. BENDING RADIUS = 75 mm
MAX. DISTANCE BETWEEN 2 PIPE CLAMPS = 1500 mm
MAX. 3 PIPE BENDS PER PIPE PIECE
(...)eingeklammerte Pos.-Nr.
Rohmaterial zur Baustellenfertigung
ITEM NOS IN BRACKETS RAW MATERIAL FOR SITE MANUFACT.

Alle Verschrb. mit Progressivring
ALL FITTINGS WITH PROGRESSIVE RING

unbearbeitete Kehlните
einseitig a=0,6x min. Blechdicke
beidseitig a=0,3x min. Blechdicke
NOT DIMENSIONED FILLET WELDS:
SINGLE SIDED a=0,6 x MIN PLATE THICKNESS
DOUBLE SIDED a=0,3 x MIN PLATE THICKNESS

Alleinigen Toleranzen nach GENERAL TOLERANCES ACC TO Brennweite nach FLAME CUTS ACC TO Schweißkonstruktion nach WELDED CONSTRUCTION ACC TO Schweißverfahren nach WELDING METHOD ACC TO Schweißverbindungen nach FUSION WELDS ACC TO Oberflächenzeichen SURFACE FINISH MARK R _a = [µm] Werkstückkanten nach COMPONENT EDGES ACC TO Skala SCALE	ISO 2768 - mK ISO 9013 - 332 ISO 13920 - B DIN EN ISO 9692-1 ISO 5817 - C ISO 13715	Maße in DIMENSIONS IN mm Darstellungsmethode PROJECTION METHOD ISO 128 Datum / DATE 11.10.2004 Gr 22.10.2004	© 2004 LOESCHE 1:50 CONNECTING PIPELINE; CPL.
--	--	---	--

Art	Anzahl	Änderungen	Datum	Name	Ort
-----	--------	------------	-------	------	-----