
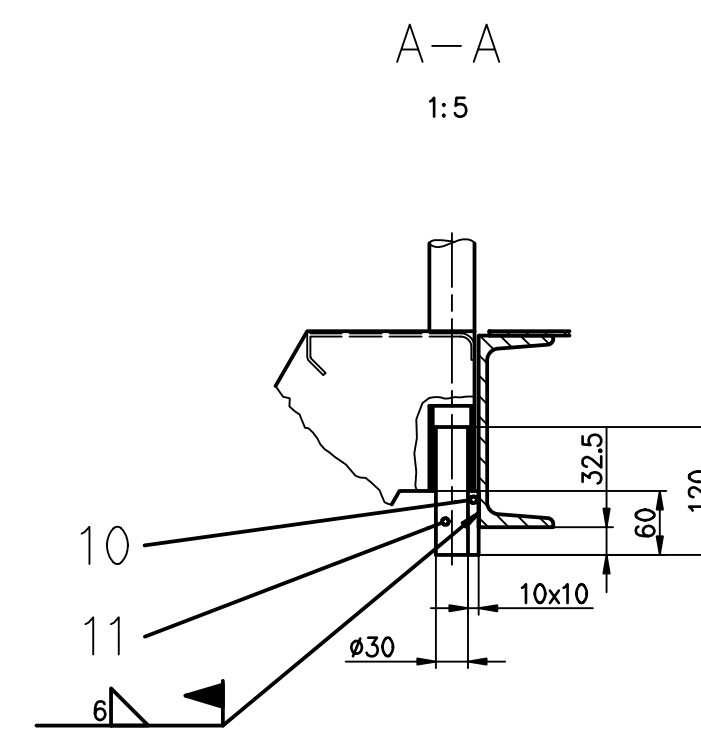


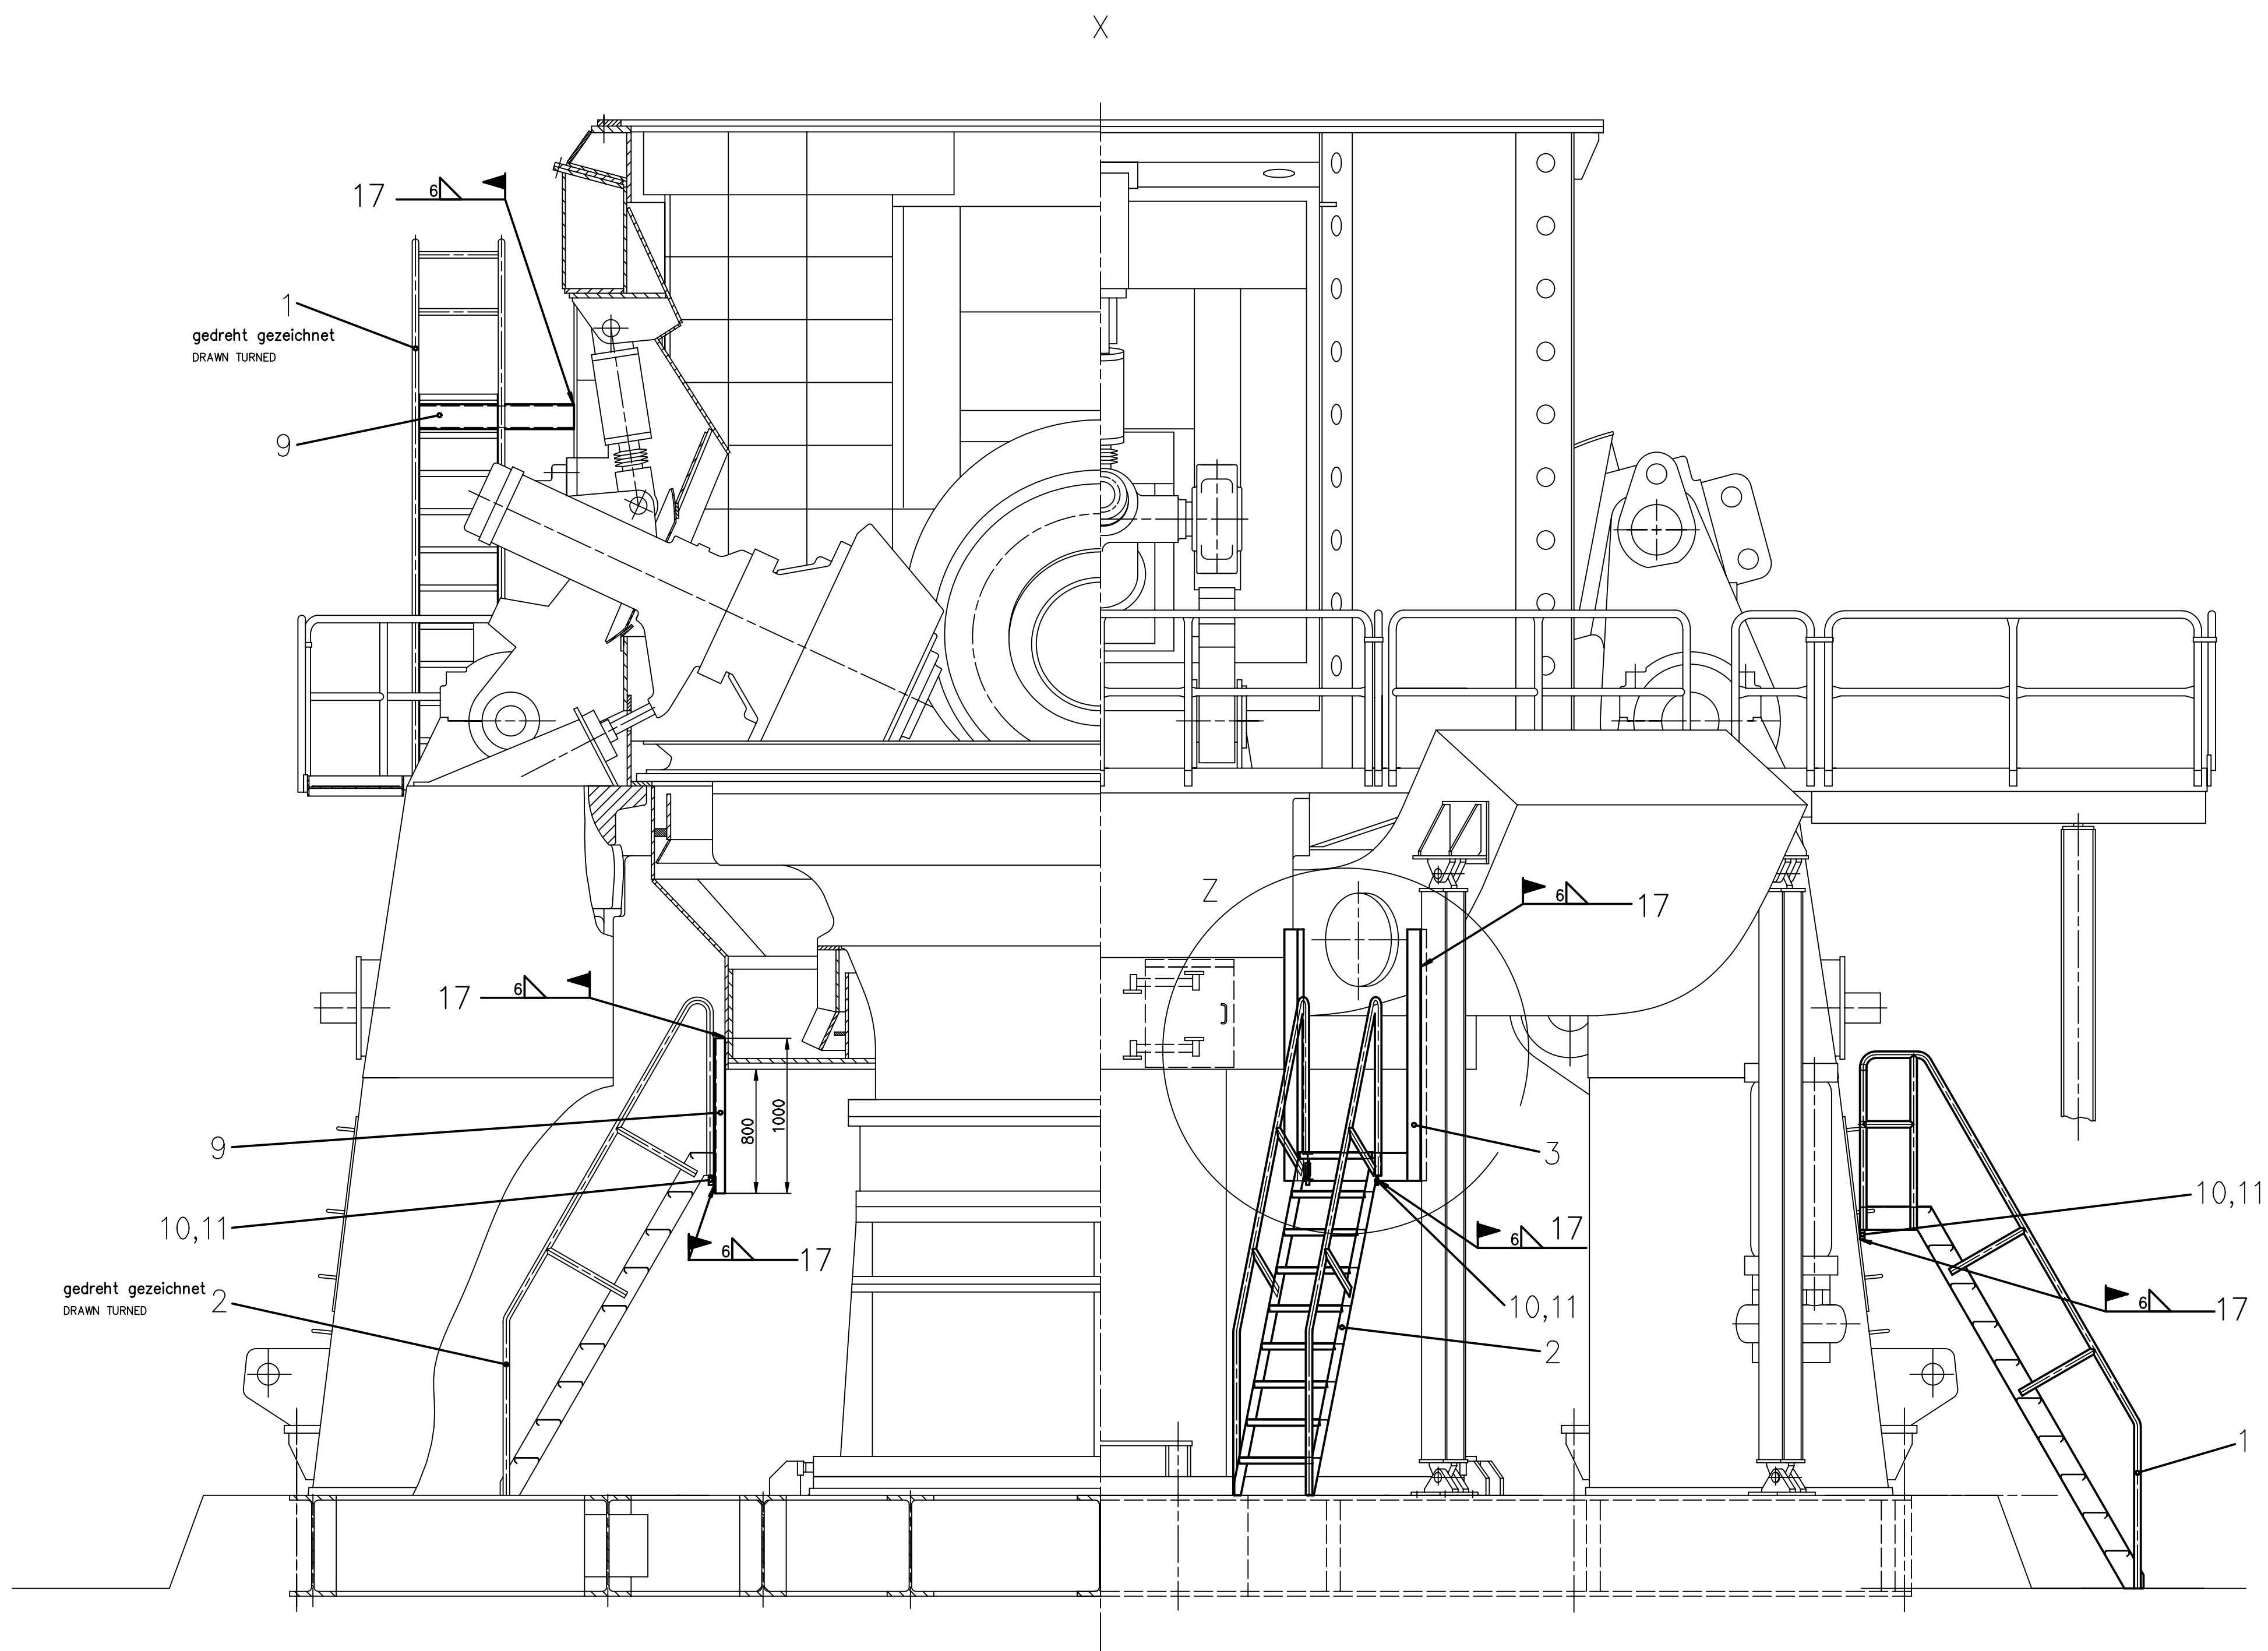

Ges.-Gew. 560,- kg		Belastet:													
Ges. 10.06.2002 FER		Erstellt für													
Gefr:		Entstanden aus													
File-Name: /cont/Lang/046319-00-0BL1															
LOESCHE 															
Potometer:															
Mittelwertwahrung R_m in μm															
Über diese Toleranzen															
nach DIN 7168 Gütegrad möglich															
Messhöhe		<table><tr><td>$\frac{R_m}{R_m \leq 50}$</td><td>$\frac{R_m}{R_m \leq 50}$</td><td>$\frac{R_m}{R_m \leq 50}$</td><td>$\frac{R_m}{R_m \leq 50}$</td><td>$\frac{R_m}{R_m \leq 50}$</td><td>$\frac{R_m}{R_m \leq 50}$</td></tr><tr><td>☒</td><td>☒</td><td>☒</td><td>☒</td><td>☒</td><td>☒</td></tr></table>		$\frac{R_m}{R_m \leq 50}$	$\frac{R_m}{R_m \leq 50}$	$\frac{R_m}{R_m \leq 50}$	$\frac{R_m}{R_m \leq 50}$	$\frac{R_m}{R_m \leq 50}$	$\frac{R_m}{R_m \leq 50}$	☒	☒	☒	☒	☒	☒
$\frac{R_m}{R_m \leq 50}$	$\frac{R_m}{R_m \leq 50}$	$\frac{R_m}{R_m \leq 50}$	$\frac{R_m}{R_m \leq 50}$	$\frac{R_m}{R_m \leq 50}$	$\frac{R_m}{R_m \leq 50}$										
☒	☒	☒	☒	☒	☒										
1:20		INSPEKTIONSLEITER: KPL.		046319-00-0	BL1										
		AUSFÜHRUNG: STAHL													
		INSPEKTION LADDER: CPL.													
pr.		Unterschrift nach DIN 3414 vorzutragen		Total 2 BL, Bl. Nr. 1											