




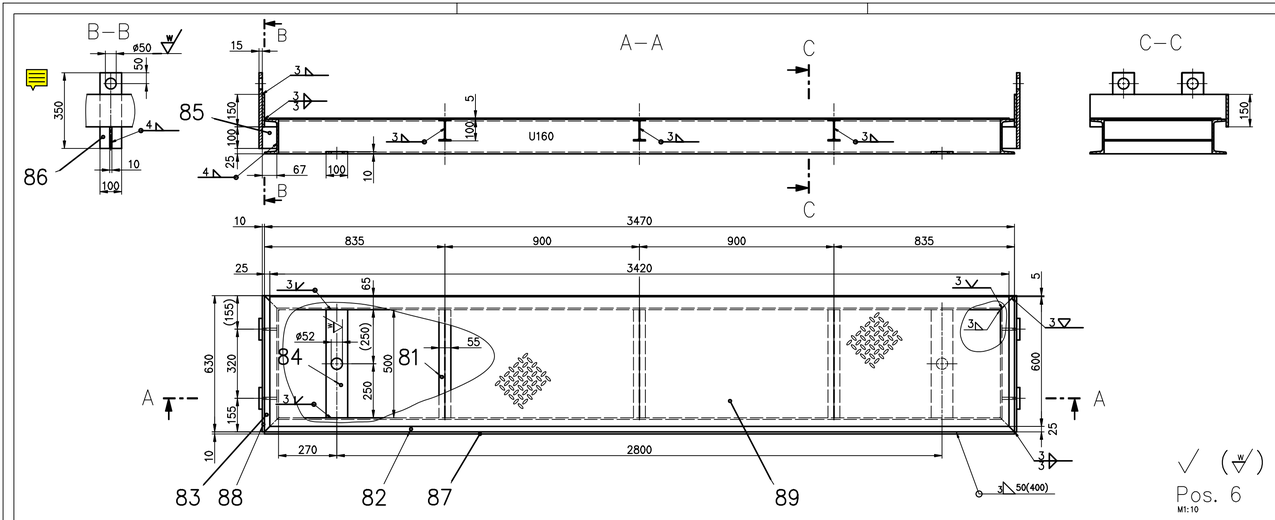


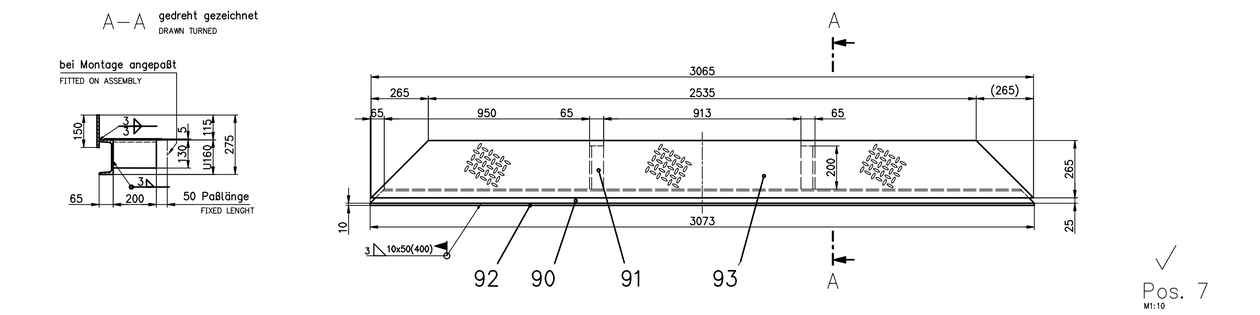


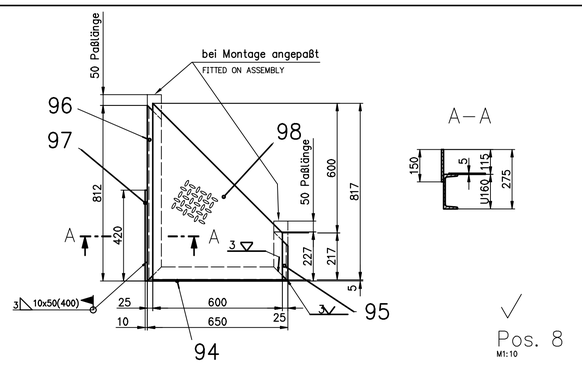


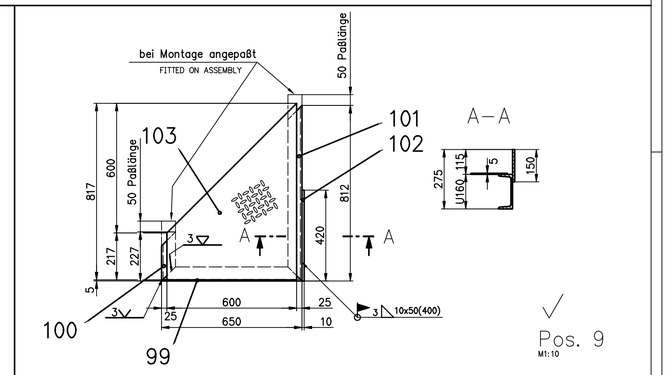


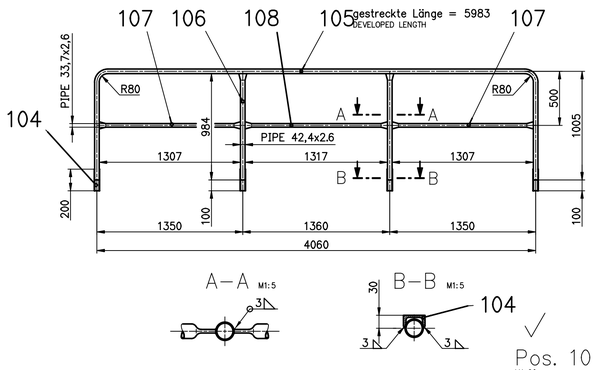

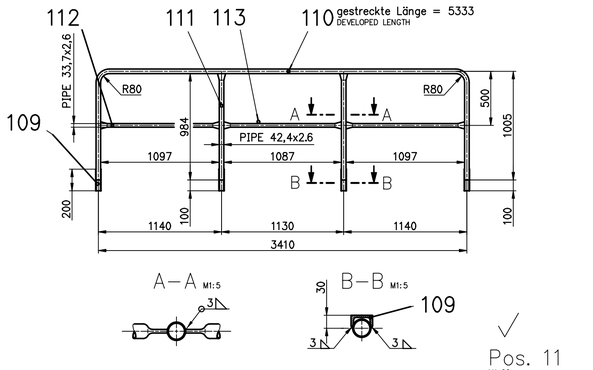

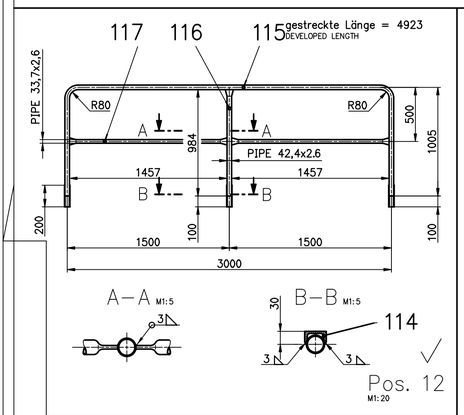

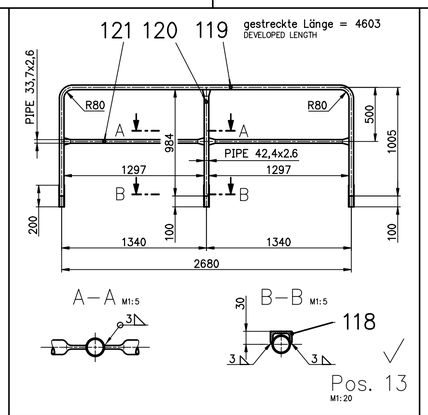

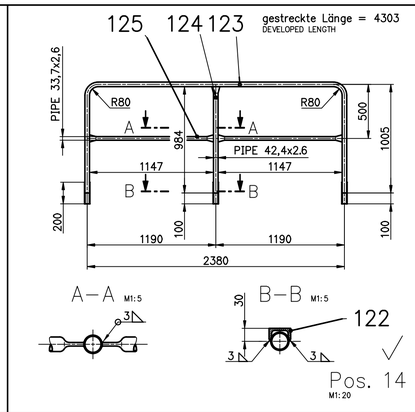

Pos.	Anz.	kg	Benennung	Norm	Werkstoff-Bez.	Werkstoff-Nr.
140	1	0,5	PIPE 33,7x2,6x257	DIN 2448	S235G2T	1.0308
139	1	5,7	PIPE 42,4x2,6x2223	DIN 2448	S235G2T	1.0308
138	2	0,7	U 50x25x200	DIN 1026	S235JR	1.0037
137	1	0,9	PIPE 33,7x2,6x442	DIN 2448	S235G2T	1.0308
136	1	6,2	PIPE 42,4x2,6x2408	DIN 2448	S235G2T	1.0308
135	2	0,7	U 50x25x200	DIN 1026	S235JR	1.0037
134	1	1,1	PIPE 33,7x2,6x527	DIN 2448	S235G2T	1.0308
133	1	6,4	PIPE 42,4x2,6x2493	DIN 2448	S235G2T	1.0308
132	2	0,7	U 50x25x200	DIN 1026	S235JR	1.0037
131	1	1,1	PIPE 33,7x2,6x557	DIN 2448	S235G2T	1.0308
130	1	6,5	PIPE 42,4x2,6x2523	DIN 2448	S235G2T	1.0308
129	2	0,7	U 50x25x200	DIN 1026	S235JR	1.0037
128	1	1,4	PIPE 33,7x2,6x707	DIN 2448	S235G2T	1.0308
127	1	6,9	PIPE 42,4x2,6x2673	DIN 2448	S235G2T	1.0308
126	2	0,7	U 50x25x200	DIN 1026	S235JR	1.0037
125	2	2,3	PIPE 33,7x2,6x1147	DIN 2448	S235G2T	1.0308
124	1	2,5	PIPE 42,4x2,6x984	DIN 2448	S235G2T	1.0308
123	1	11,1	PIPE 42,4x2,6x4303	DIN 2448	S235G2T	1.0308
122	3	0,7	U 50x25x200	DIN 1026	S235JR	1.0037
121	2	2,8	PIPE 33,7x2,6x1297	DIN 2448	S235G2T	1.0308
120	1	2,5	PIPE 42,4x2,6x984	DIN 2448	S235G2T	1.0308
119	1	11,1	PIPE 42,4x2,6x4603	DIN 2448	S235G2T	1.0308
118	3	0,7	U 50x25x200	DIN 1026	S235JR	1.0037
117	2	2,9	PIPE 33,7x2,6x1457	DIN 2448	S235G2T	1.0308
116	1	2,5	PIPE 42,4x2,6x984	DIN 2448	S235G2T	1.0308
115	1	12,7	PIPE 42,4x2,6x4923	DIN 2448	S235G2T	1.0308
114	3	0,7	U 50x25x200	DIN 1026	S235JR	1.0037
113	1	2,2	PIPE 33,7x2,6x1087	DIN 2448	S235G2T	1.0308
112	2	2,2	PIPE 33,7x2,6x1097	DIN 2448	S235G2T	1.0308
111	2	2,5	PIPE 42,4x2,6x984	DIN 2448	S235G2T	1.0308
110	1	13,7	PIPE 42,4x2,6x5333	DIN 2448	S235G2T	1.0308
109	4	0,7	U 50x25x200	DIN 1026	S235JR	1.0037
108	1	2,5	PIPE 33,7x2,6x1317	DIN 2448	S235G2T	1.0308
107	2	2,5	PIPE 33,7x2,6x1307	DIN 2448	S235G2T	1.0308
106	2	2,5	PIPE 42,4x2,6x984	DIN 2448	S235G2T	1.0308
105	1	15,4	PIPE 42,4x2,6x5983	DIN 2448	S235G2T	1.0308
104	4	0,7	U 50x25x200	DIN 1026	S235JR	1.0037
103	1	13,0	PLATE T5x600x817	DIN 59220	S235JRG2	1.0038
102	1	4,9	FLAT 150x10x420	DIN 1017	S235JRG2	1.0038
101	1	16,2	U 160x862	DIN 1026	S235JR	1.0037
100	1	5,2	U 160x277	DIN 1026	S235JR	1.0037
99	1	12,2	U 160x650	DIN 1026	S235JR	1.0037
98	1	13,0	PLATE T5x600x817	DIN 59220	S235JRG2	1.0038
97	1	4,9	FLAT 150x10x420	DIN 1017	S235JRG2	1.0038
96	1	16,2	U 160x862	DIN 1026	S235JR	1.0037
95	1	5,2	U 160x277	DIN 1026	S235JR	1.0037
94	1	12,2	U 160x650	DIN 1026	S235JR	1.0037
93	1	30,8	PLATE T5x265x3065	DIN 59220	S235JRG2	1.0038
92	1	36,1	FLAT 150x10x3073	DIN 1017	S235JRG2	1.0038
91	2	3,8	L 130x65x10x250	EN 10056-T1	S235JRG1	1.0036
90	1	57,7	U 160x3073	DIN 1026	S235JR	1.0037
89	1	84,7	PLATE T5x600x3420	DIN 59220	S235JRG2	1.0038
88	2	7,4	FLAT 150x10x630	DIN 1017	S235JRG2	1.0038
87	1	40,8	FLAT 150x10x3470	DIN 1017	S235JRG2	1.0038
86	4	4,1	FLAT 100x15x350	DIN 1017	S235JRG2	1.0038
85	4	0,5	FLAT 100x10x67	DIN 1017	S235JRG2	1.0038
84	2	3,9	FLAT 100x10x500	DIN 1017	S235JRG2	1.0038
83	2	11,8	U 160x630	DIN 1026	S235JR	1.0037
82	2	65,2	U 160x3470	DIN 1026	S235JR	1.0037
81	3	4,1	IPE 100x500	DIN 1025	S235JR	1.0037

Schweißnahtvorbereitung nach EN 29692
EDGE PREPARATION FOR WELDING IN ACCORDANCE WITH EN 29692

Freimaßtoleranzen für Schweißkonstruktionen nach EN ISO 13920 Genauigkeitsgrad B
GENERAL TOLERANCES FOR WELDED CONSTRUCTIONS IN ACCORDANCE WITH EN ISO 13920 DEGREE OF PRECISION B

unbemaßte Kehlnähte
einseitig a=0,6x min. Blechdicke
beidseitig a=0,3x min. Blechdicke
NOT DIMENSIONED FILLET WELDS:
SINGLE SIDED a=0,6 x MIN PLATE THICKNESS
DOUBLE SIDED a=0,3 x MIN PLATE THICKNESS

Ges.-Gew. | Betreff:
Ges. 04.11.2002 Goe | Ersatz für
Gepr. 16.12.2002 Ad | Entstanden aus
File-Name:
Plotdatum: 16.12.02
Oberflächenzeichen Mittenrauwert R_a in µm. Masse ohne Toleranzangaben nach DIN 7168 Guetegrad mittel. Weiteres Zustand: Ra ≤ 50 | Ra ≤ 12,5 | Ra ≤ 3,2 | Ra ≤ 0,8 | Ra ≤ 0,1

LOESCHE

CAD

Maßstab 1:10

MUEHLENBUEHNE; KPL.
MILL PLATFORM; CPL.

055349-00-0 BL3

Urheberschutz nach DIN 34 vorbehalten | Total: | Bl. | Bl.Nr.

Ael	Anzahl	EDV	Mikro	Änderungen	Datum	Name	Gepr.

GENTITLE-LL