

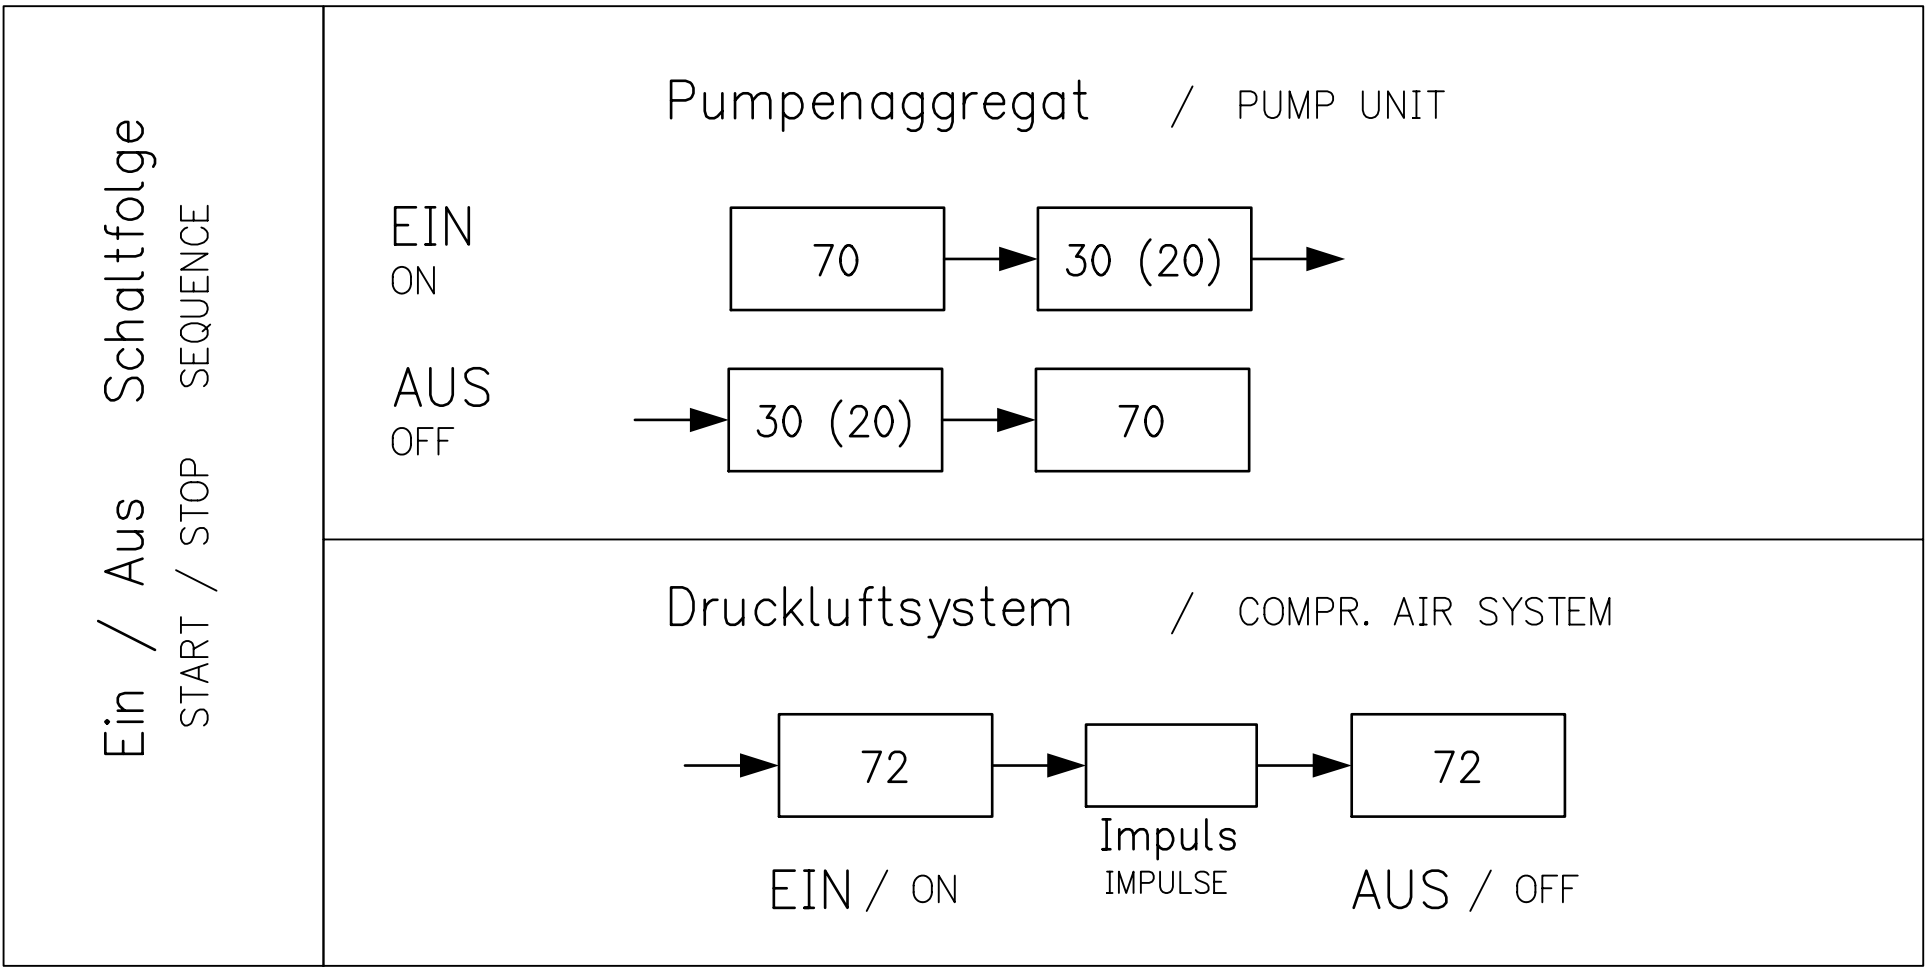
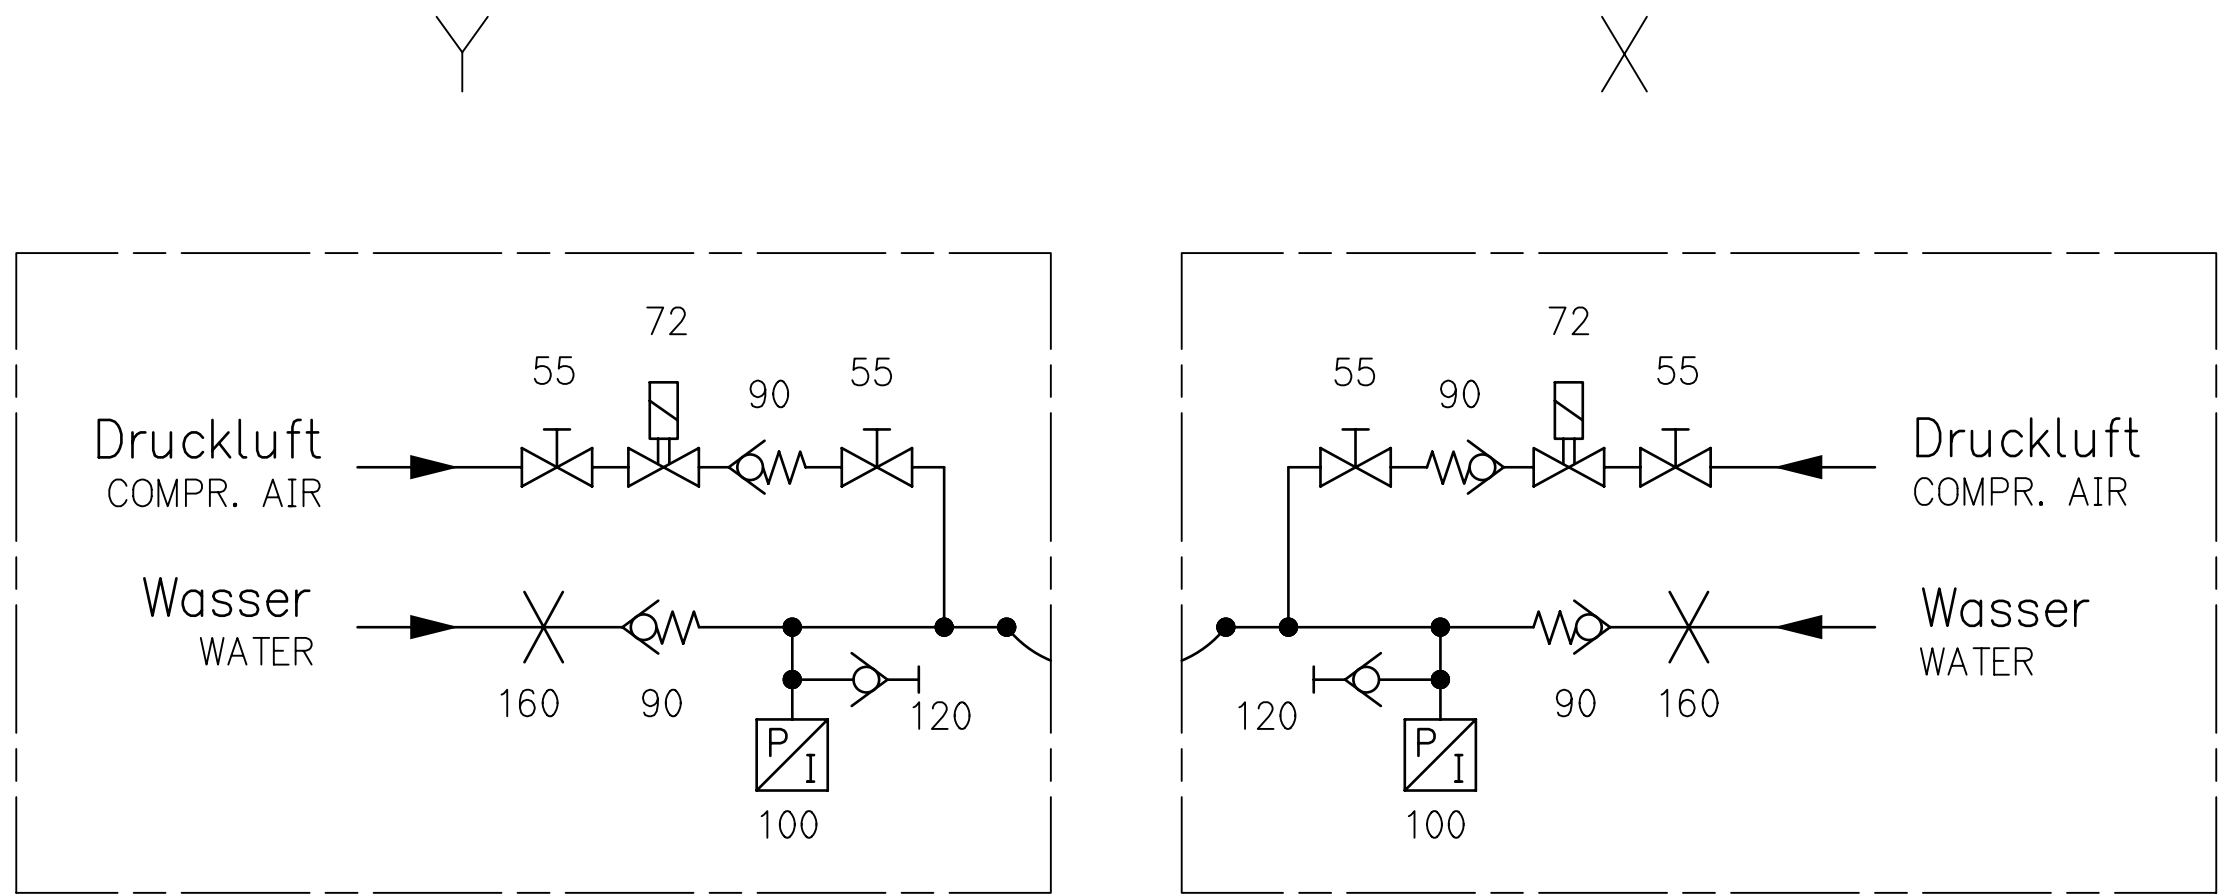
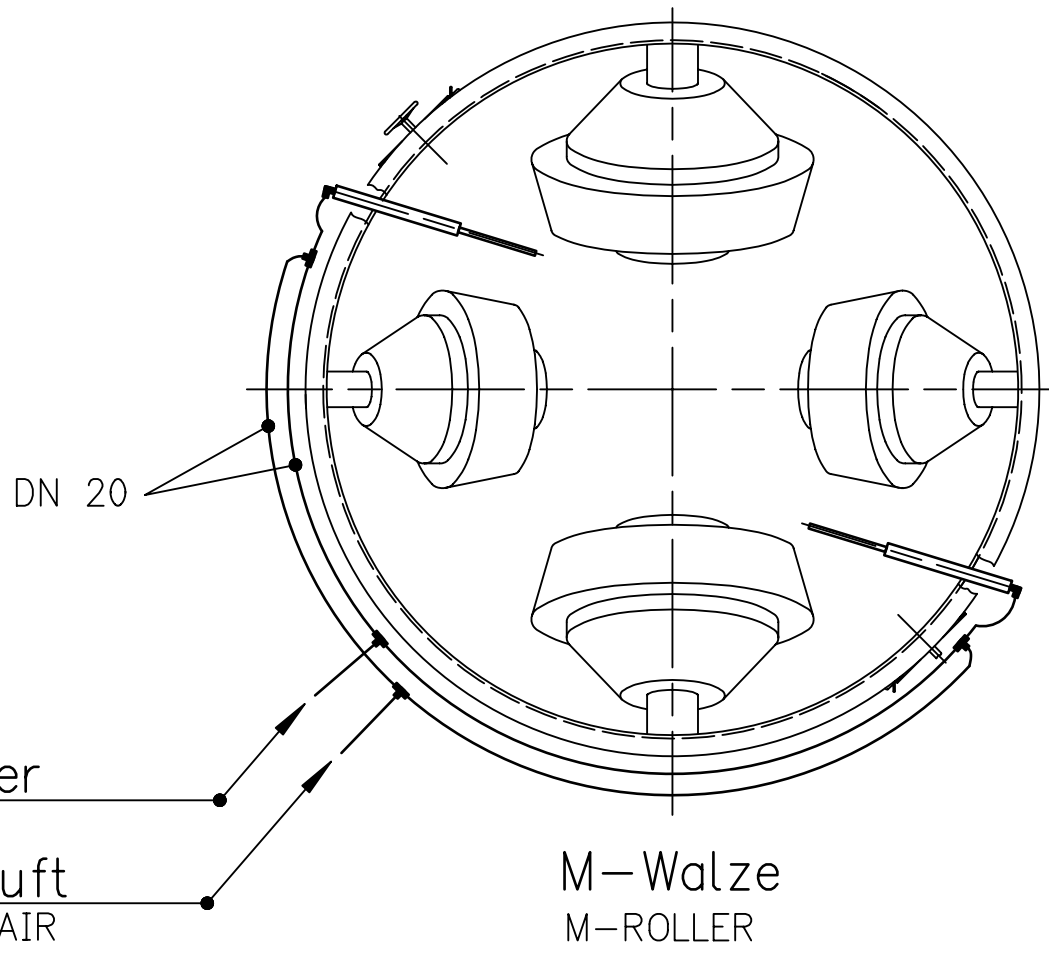
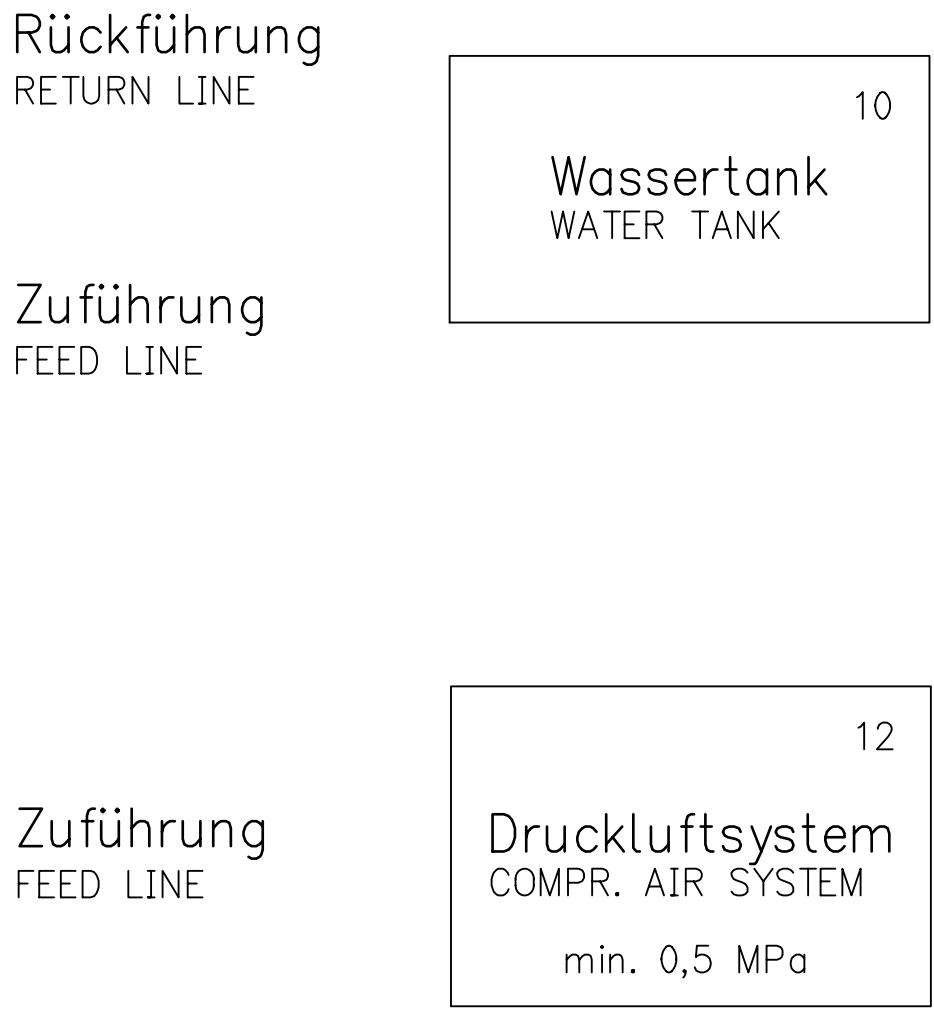


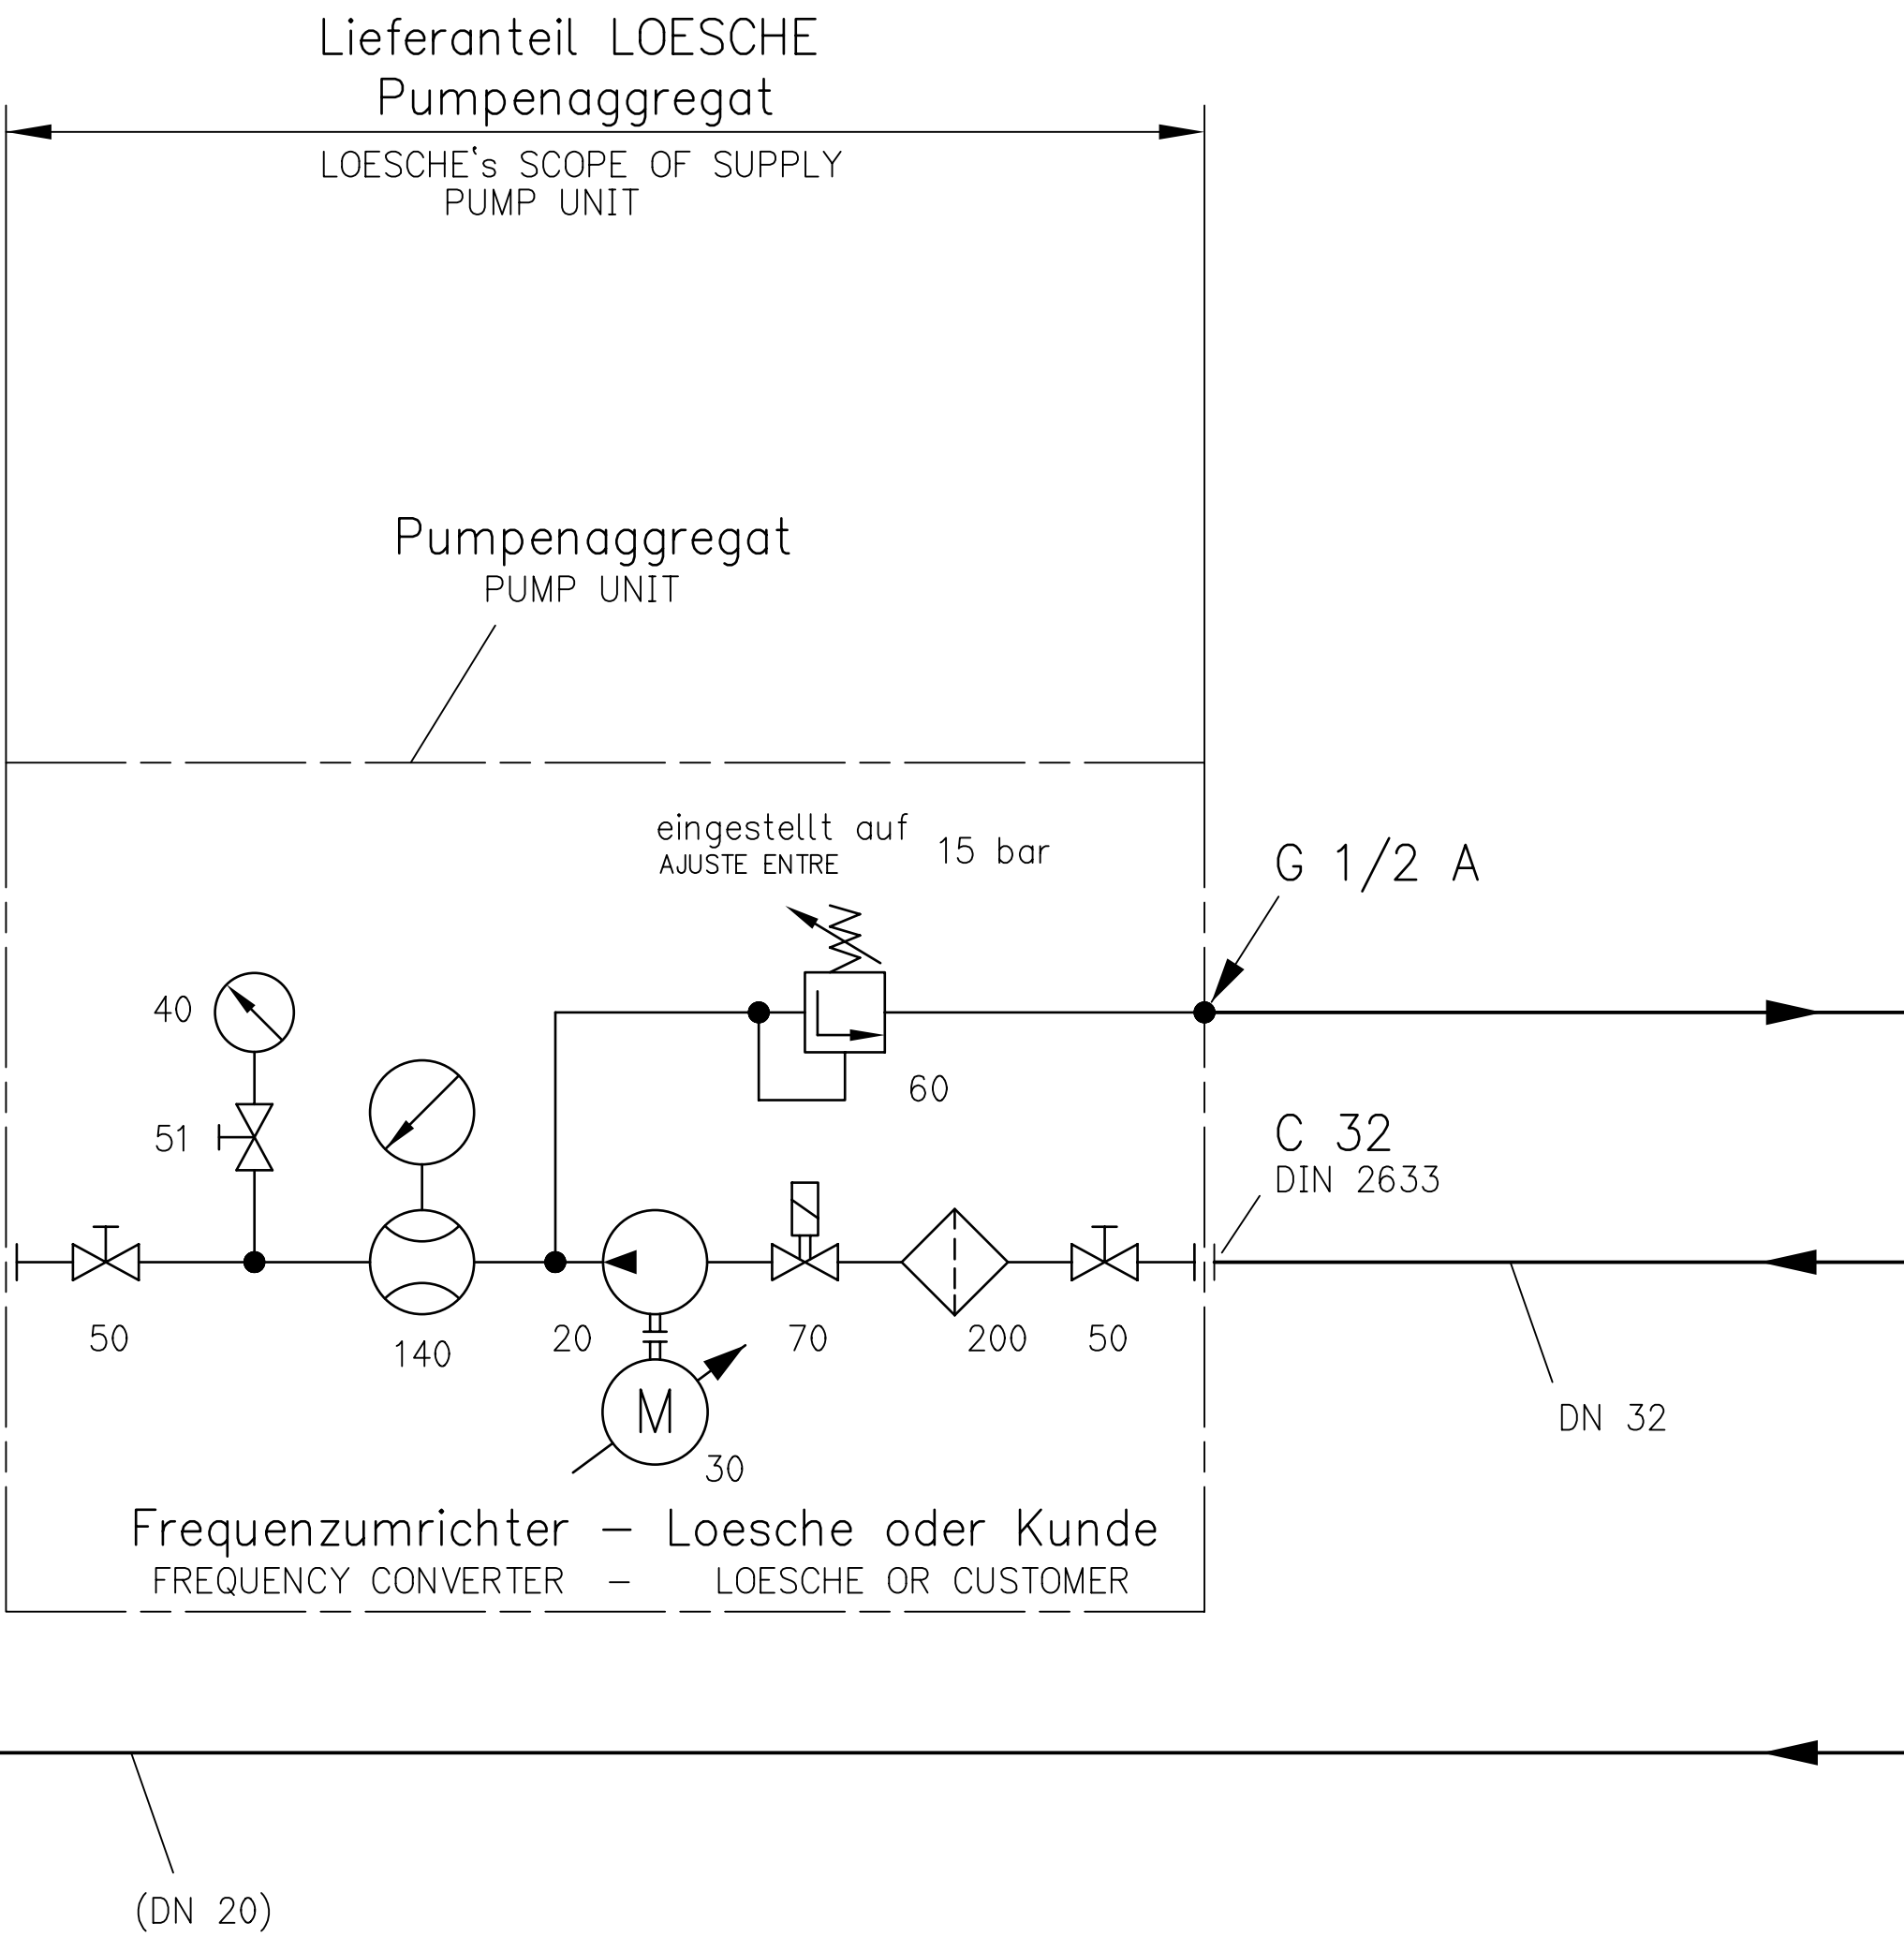

10	Wassertank	WATERTANK
12	Druckluftsystem	COMPRESSION AIR SYSTEM
20	Pumpe	PUMP
30	Elektromotor	ELECTRIC MOTOR
--	frequenzgeregelt	FREQUENCY CONTROLLED
40	Manometer	PRESSURE GAUGE
50	Absperrorgan	CLOSURE DEVICE
51	Absperrorgan	CLOSURE DEVICE
55	Absperrorgan	CLOSURE DEVICE
60	Druckbegrenzungsventil	PRESS.RELIEF VALVE
70	Magnetsteuerventil	SOLENOID CONTROL VALVE
72	Magnetsteuerventil	SOLENOID CONTROL VALVE
90	Rückschlagventil	CHECK VALVE
100	Drucktransmitter	PRESSURE TRANSMITTER
120	Meßstelle	MEASURING POINT
140	Durchflußmesser	FLOWMETER
160	Blende	DIAPHRAGM
200	Filter	FILTER

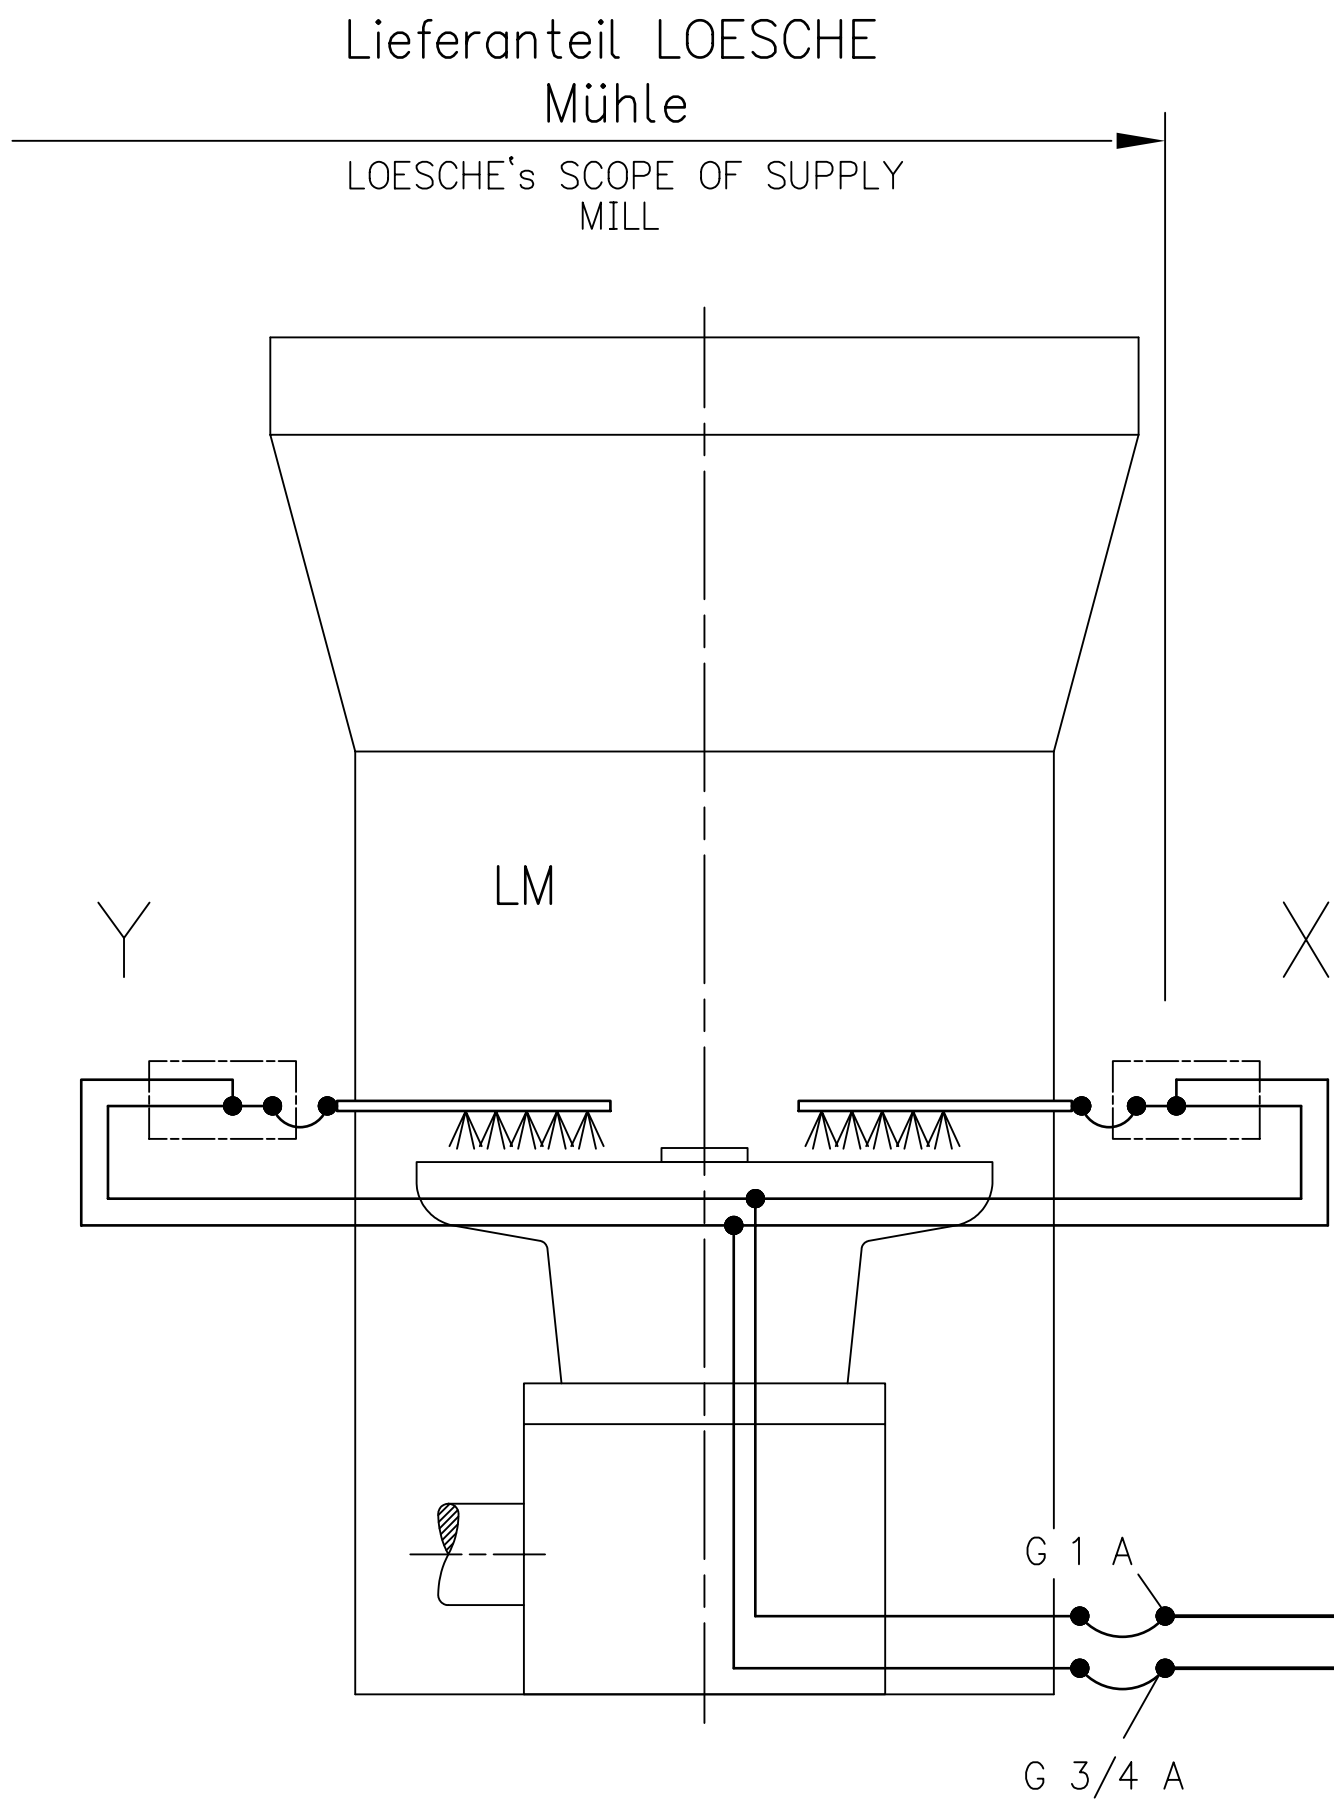

S-Walze
S-ROLLER

Zuleitung annähernd mittig zwischen beiden Einspritzpunkten
TUBE CONNECTION NEARLY IN THE MIDDLE OF THE TWO LOCATIONS OF INJECTION

a	1	Symbole überarbeitet	07.08.2003	Fer	SL
AeI	Anzahl	Änderungen	Datum	Name	Gepr.

Ges.-Gew.				Plotdatum		08.08.2003		Betreff:		LOESCHE		
Gez.		21.02.2003 Goe		Ersatz für								
Gepr.		12.03.2003 SL		Entstanden aus								
Allgemeintoleranzen nach ISO 2768 – mK				Schutzvermerk nach ISO 16016								
Oberflächenzeichen												CAD
Mittenrauhwert R_a in μm												
Maßstab		SCHEMA: MAHLBETTBERIESELUNG								901812-00-2		
1:1		4 m3/h										
SCHEME: GRINDING-BED SPRINKLER								Total		Bl./Bl.Nr.		